
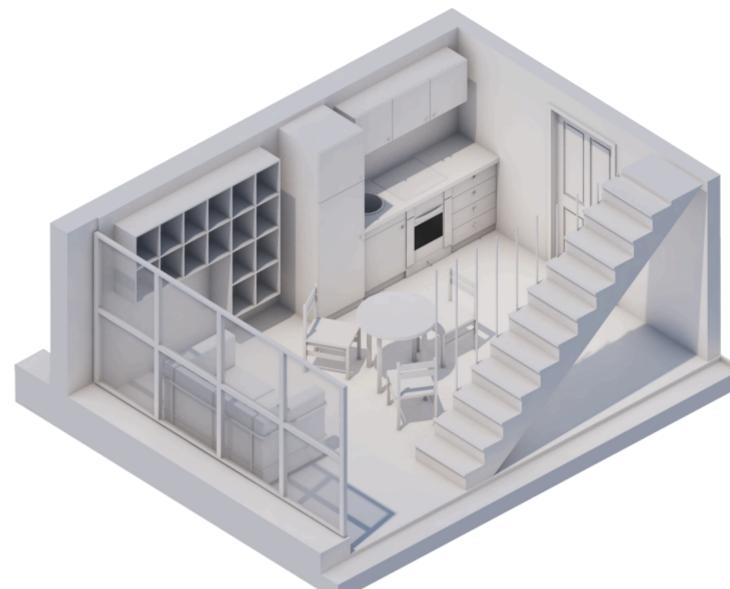


# Suite d'albergo

Questo progetto di suite d'albergo pensata per due ospiti si sviluppa su due piani, per un totale di 50 mq.

Il punto forte di questa particolare suite d'hotel riguarda gli interni dallo stile elegante e pulito che cercano di unire contemporaneamente elementi che abbiano un forte richiamo naturale ma senza sfociare nel "rustico". Si è riuscito a creare quindi una perfetta armonia negli interni

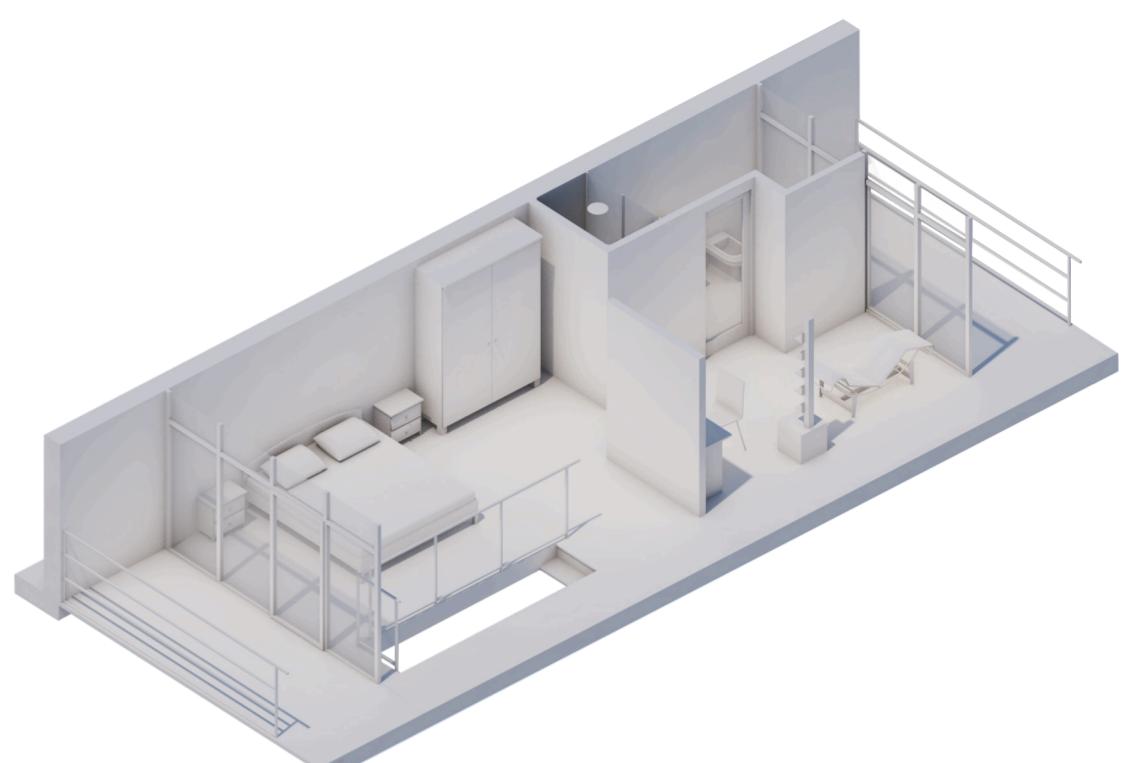

## PRIMO PIANO

L'ingresso situato a piano terra introduce l'ospite nella sala da pranzo, dotata di un piano cucina sulla parete destra e di un tavolo da tre posti. Sono inoltre presenti una capiente libreria e un divanetto. La sala è bene illuminata dalla grande vetrata. Sulla parete sinistra sono invece presenti le scale che portano al secondo piano.


## SECONDO PIANO

Le scale portano alla zona notte della suite, composta da un letto matrimoniale accompagnato da due comodini e da un armadio, la quale viene illuminata da una delle due grandi presenti. Il bagno e un piccolo studio compongono la seconda metà del secondo piano, anch'essi ben illuminati dall'altra grande vetrata. Entrambe le vetrate comunicano con due piccoli balconcini



PARETI

Rivestimento in pietre scure

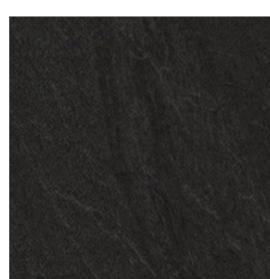

PAVIMENTO BAGNO

Piastrelle di pietra liscia




PARETI BAGNO

Marmo con venature gialle



PAVIMENTI

Marmo con venature grige

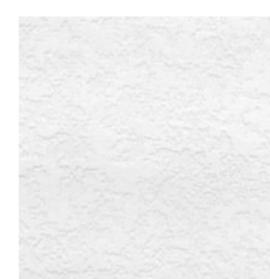

PARETI

intonaco bianco




Sezione prospettica



# Disegni tecnici


---

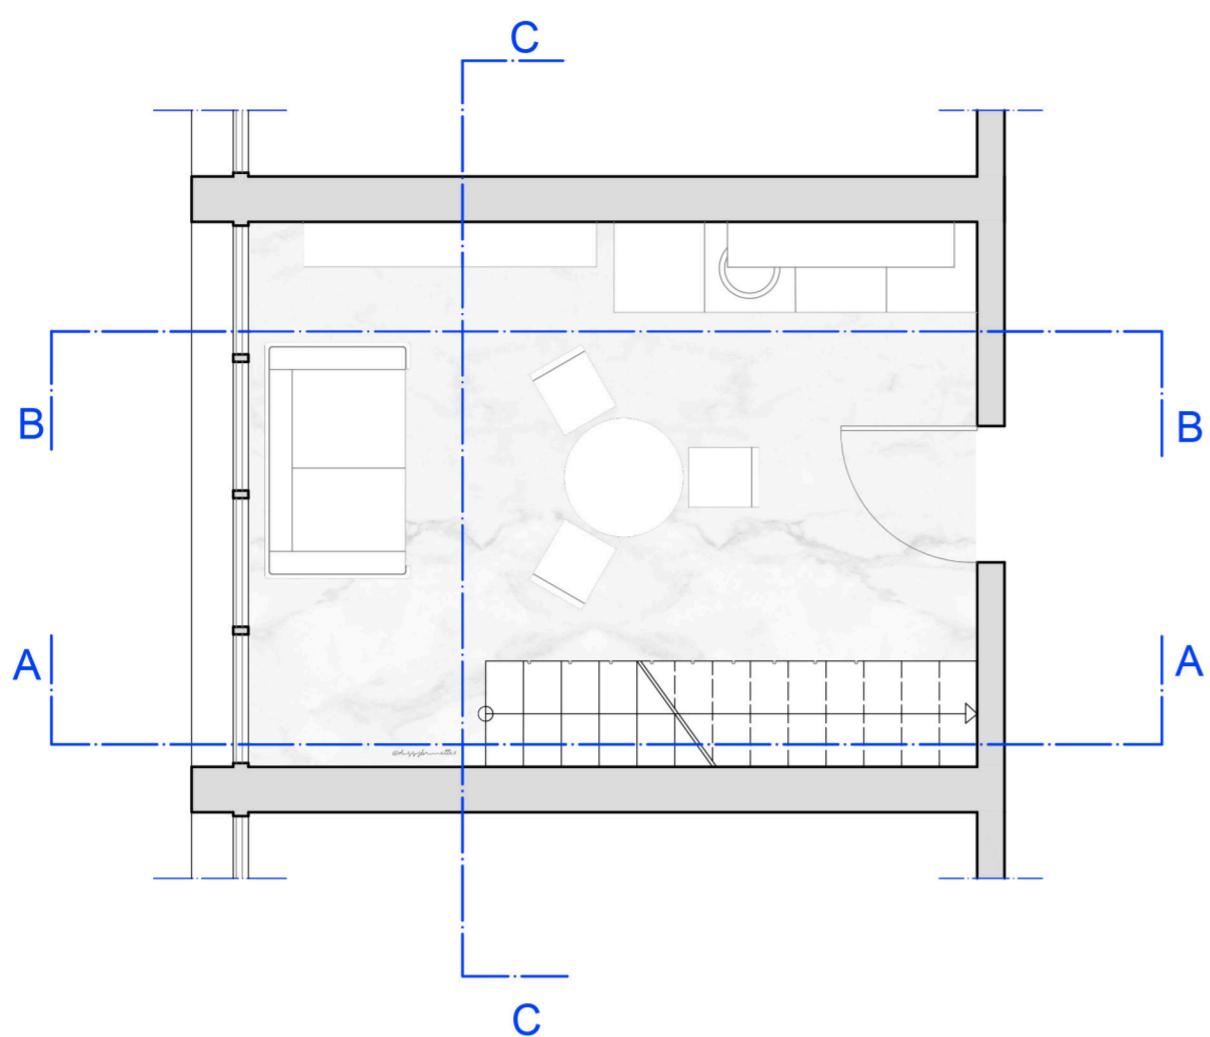


Pianta piano terra scala 1:50



Sezione C-C 1:50

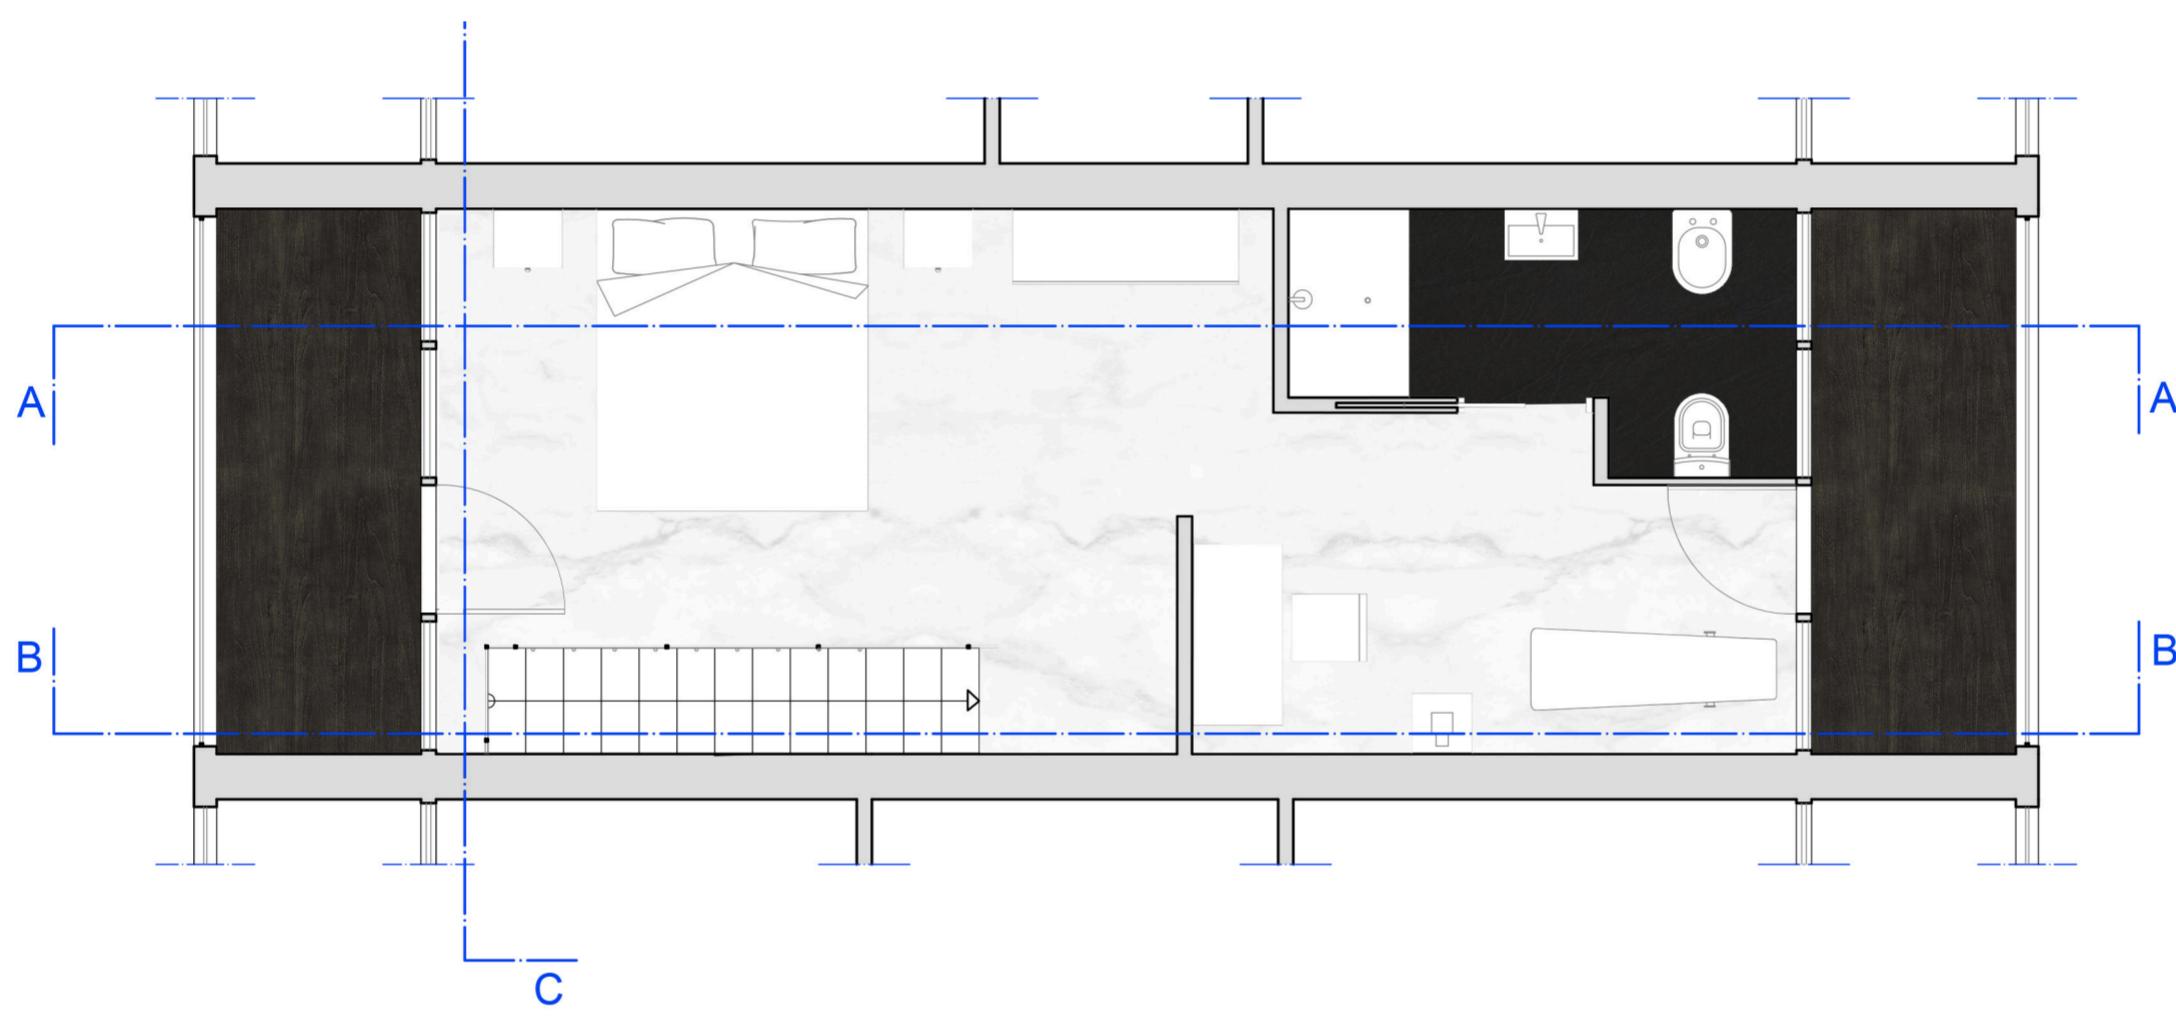


Pianta secondo piano scala 1:50

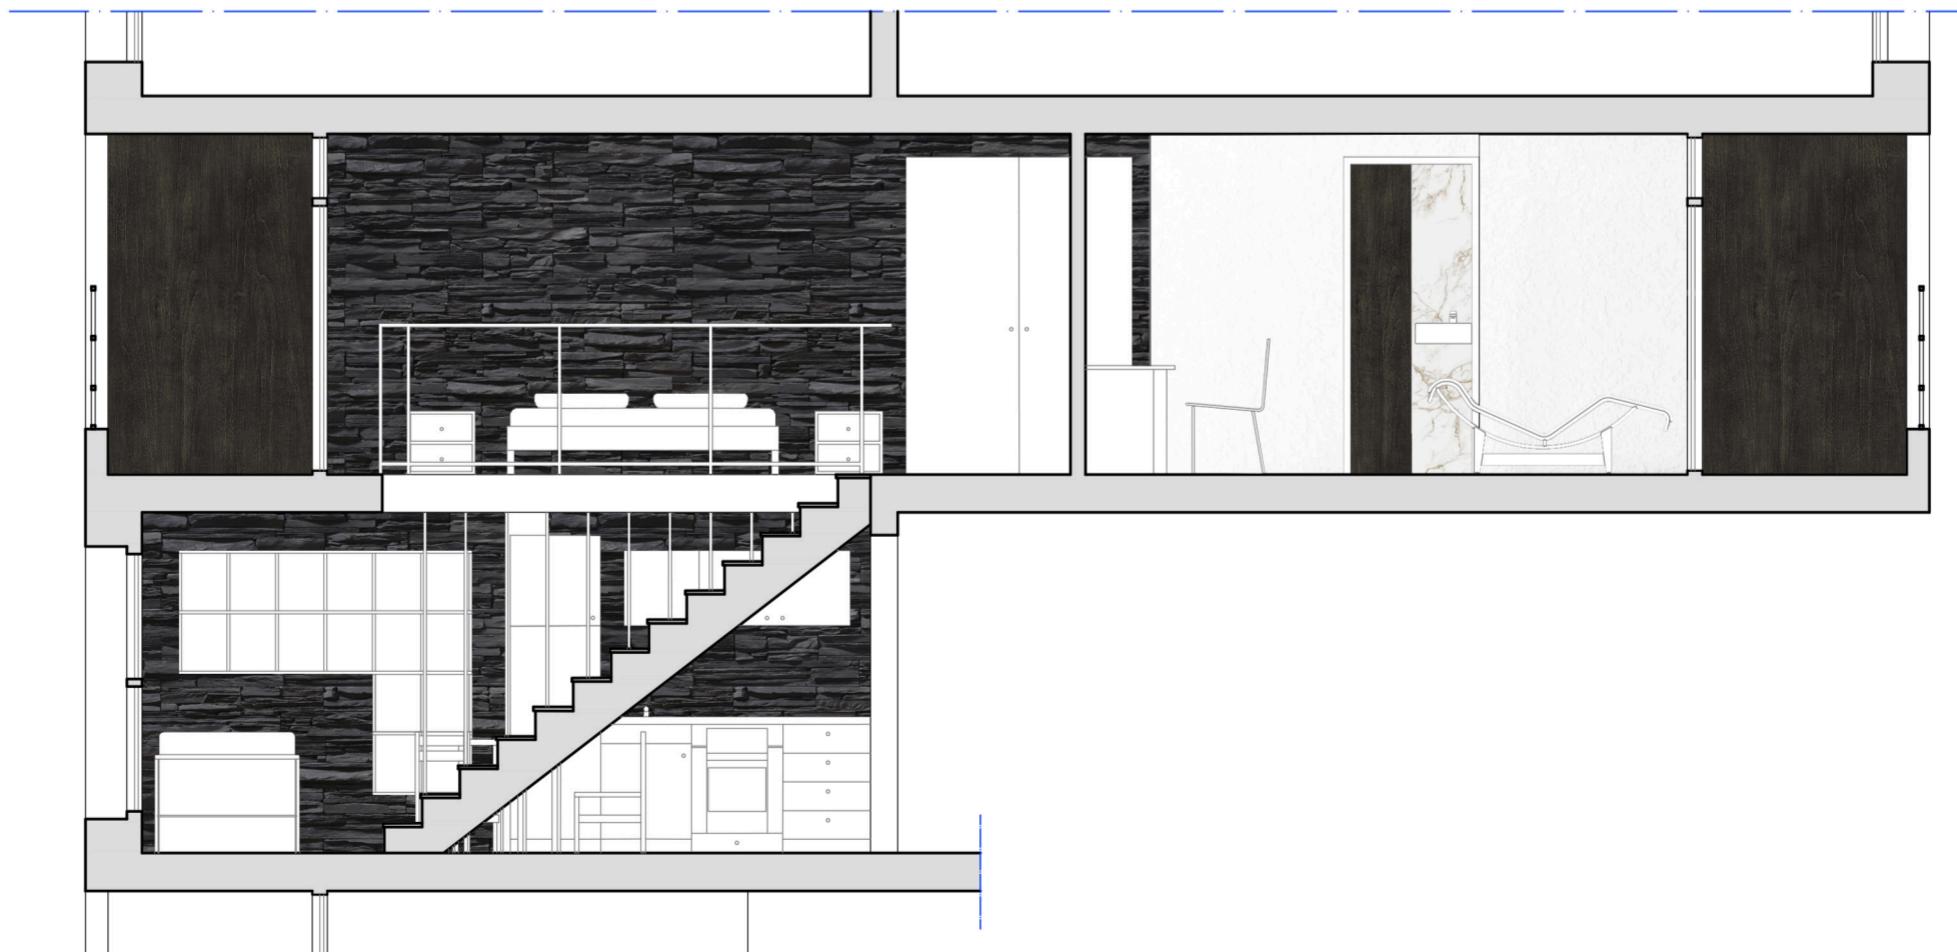

Sezione A-A scala 1:50



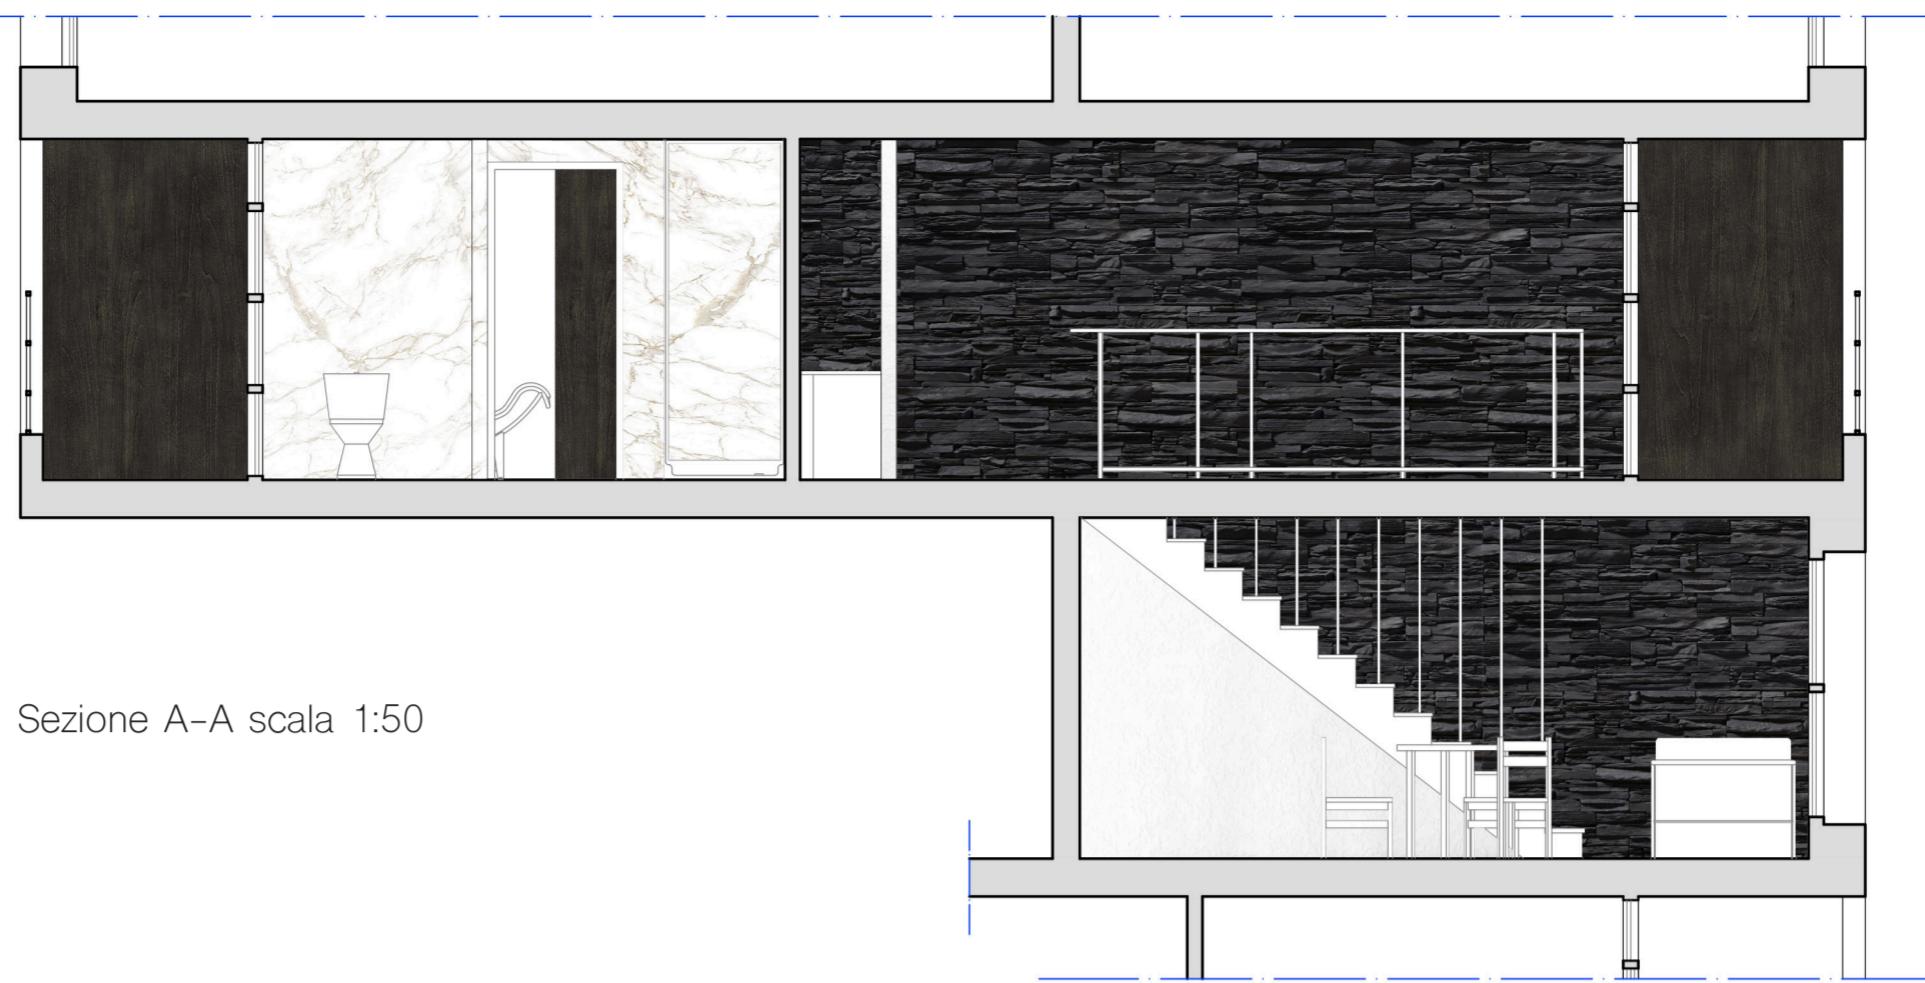

## Oggetto personale

La libreria posta nello studio della suite è semplice e leggera, composta da pochi pezzi e facile da assemblare, il suo peso leggero consente di essere spostata per l'ambiente senza faticare.

La libreria si compone di una base cubica in legno con un foro cilindrico. L'asta di alluminio, su cui vengono fissati i ripiani per i libri con dei chiodi, ha saldato alla base un cilindro di ferro delle stesse dimensioni del foro, in modo da permetterne l'incastro





ASTA E SOSTEGNI

Alluminio




CILINDRO

Ferro

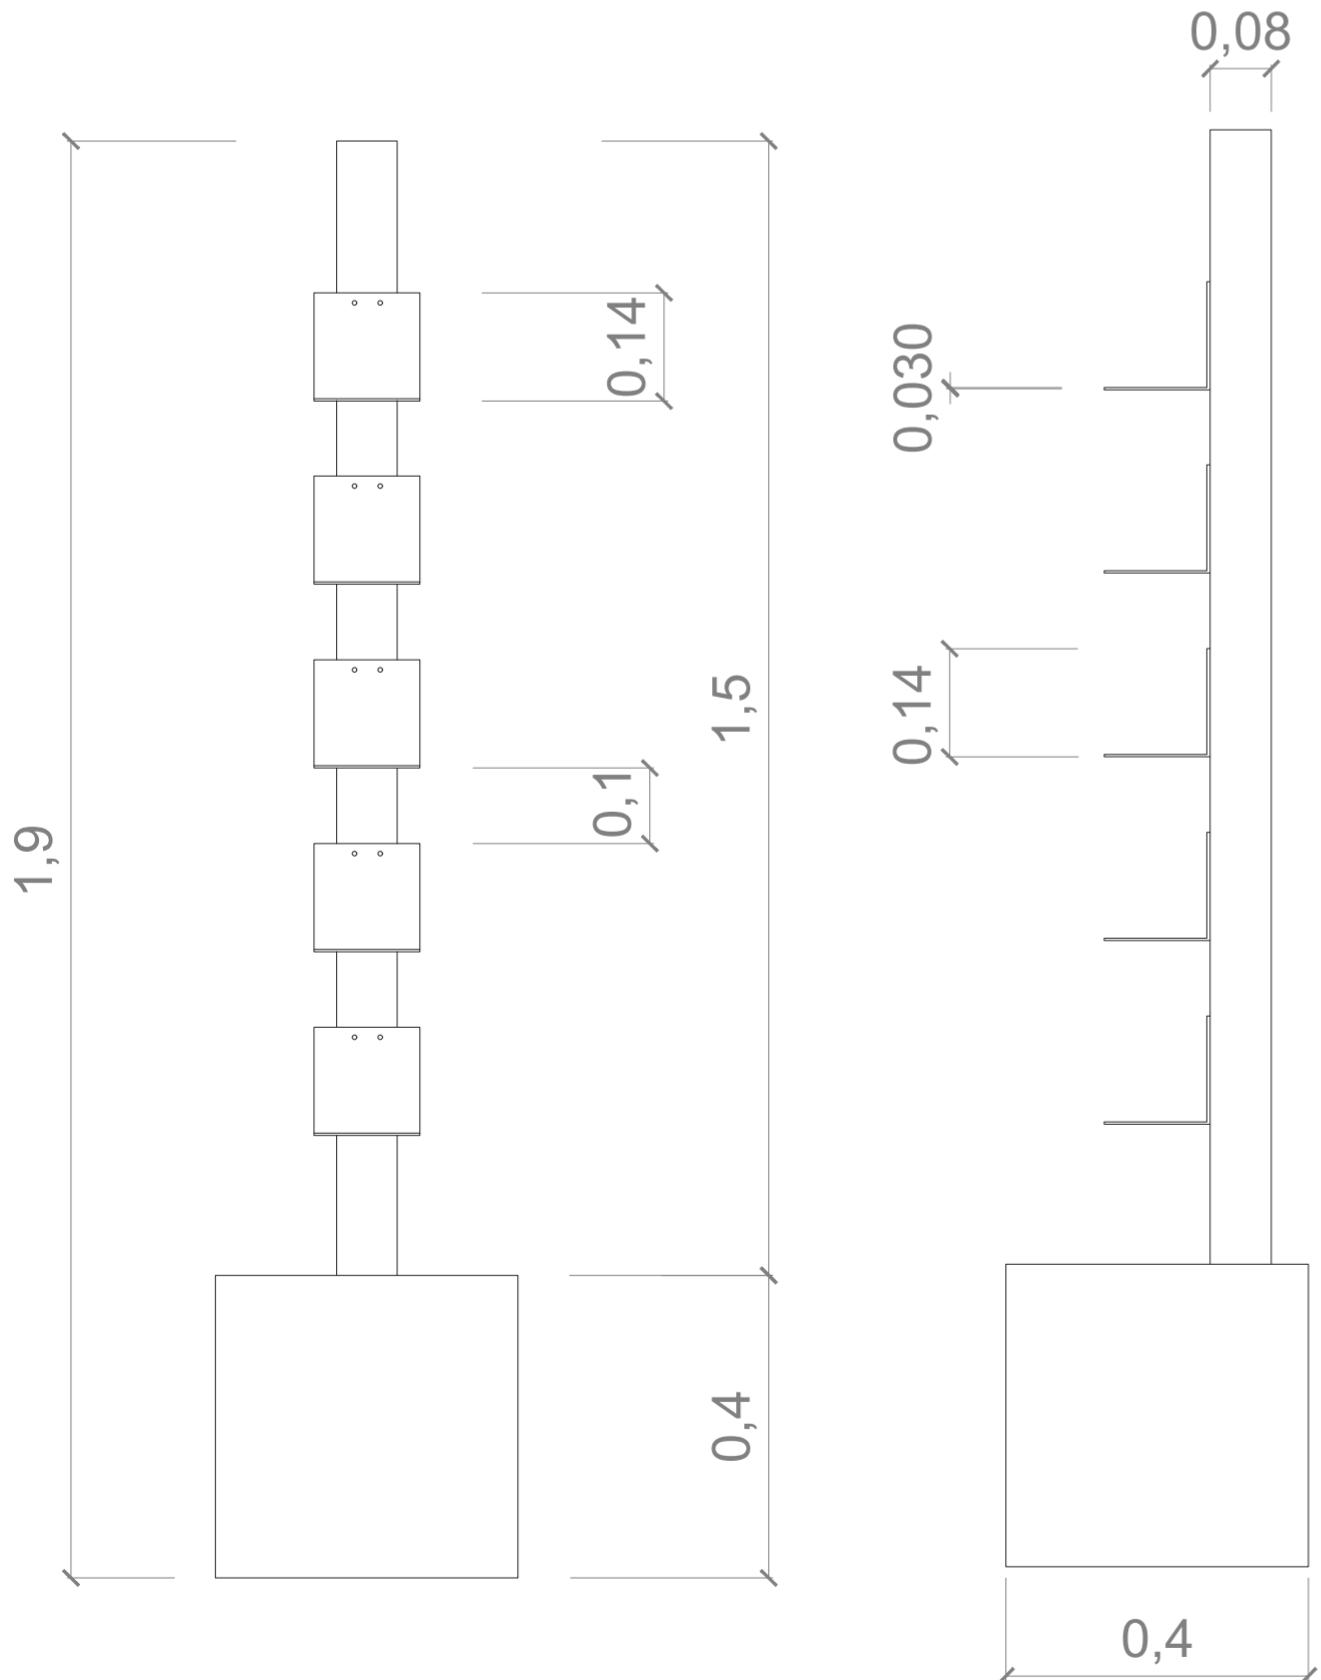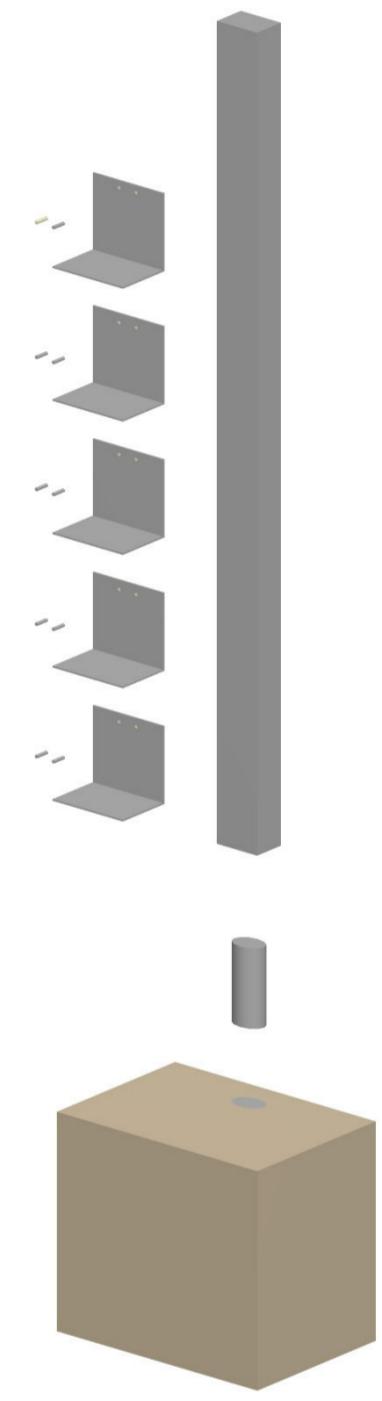

Prospetto frontale scala 1:10

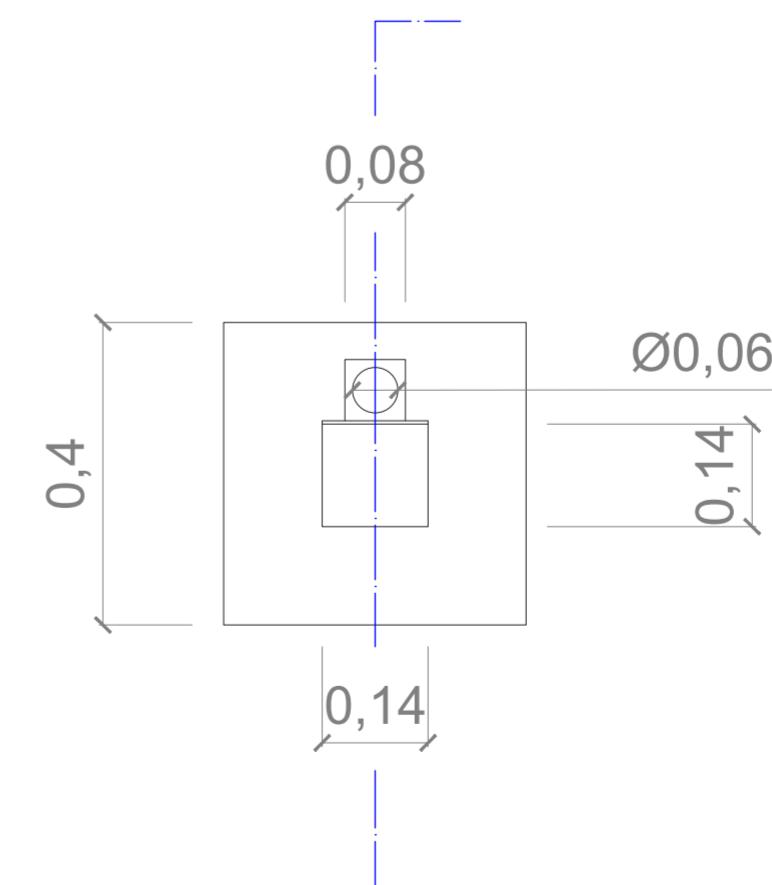

Vista zenitale scala 1:10

sezione longitudinale della base

Prospetto laterale 1:10

