

# PROGETTO DI UNA SUITE D'ALBERGO


## MATTIA FRANZETTI



### IL PROGETTO



Questo progetto si propone di sviluppare un piccolo appartamento all'interno di un edificio ricettivo. L'appartamento misura circa 50 mq e si sviluppa su due livelli secondo uno schema modulare e precostituito. La selezione e i criteri di progetto sono liberi e pertanto il progettista avrà la facoltà di caratterizzare questi spazi secondo il proprio gusto e in accordo con la tipologia abitativa.

### PIANTA PIANO AB 1:50

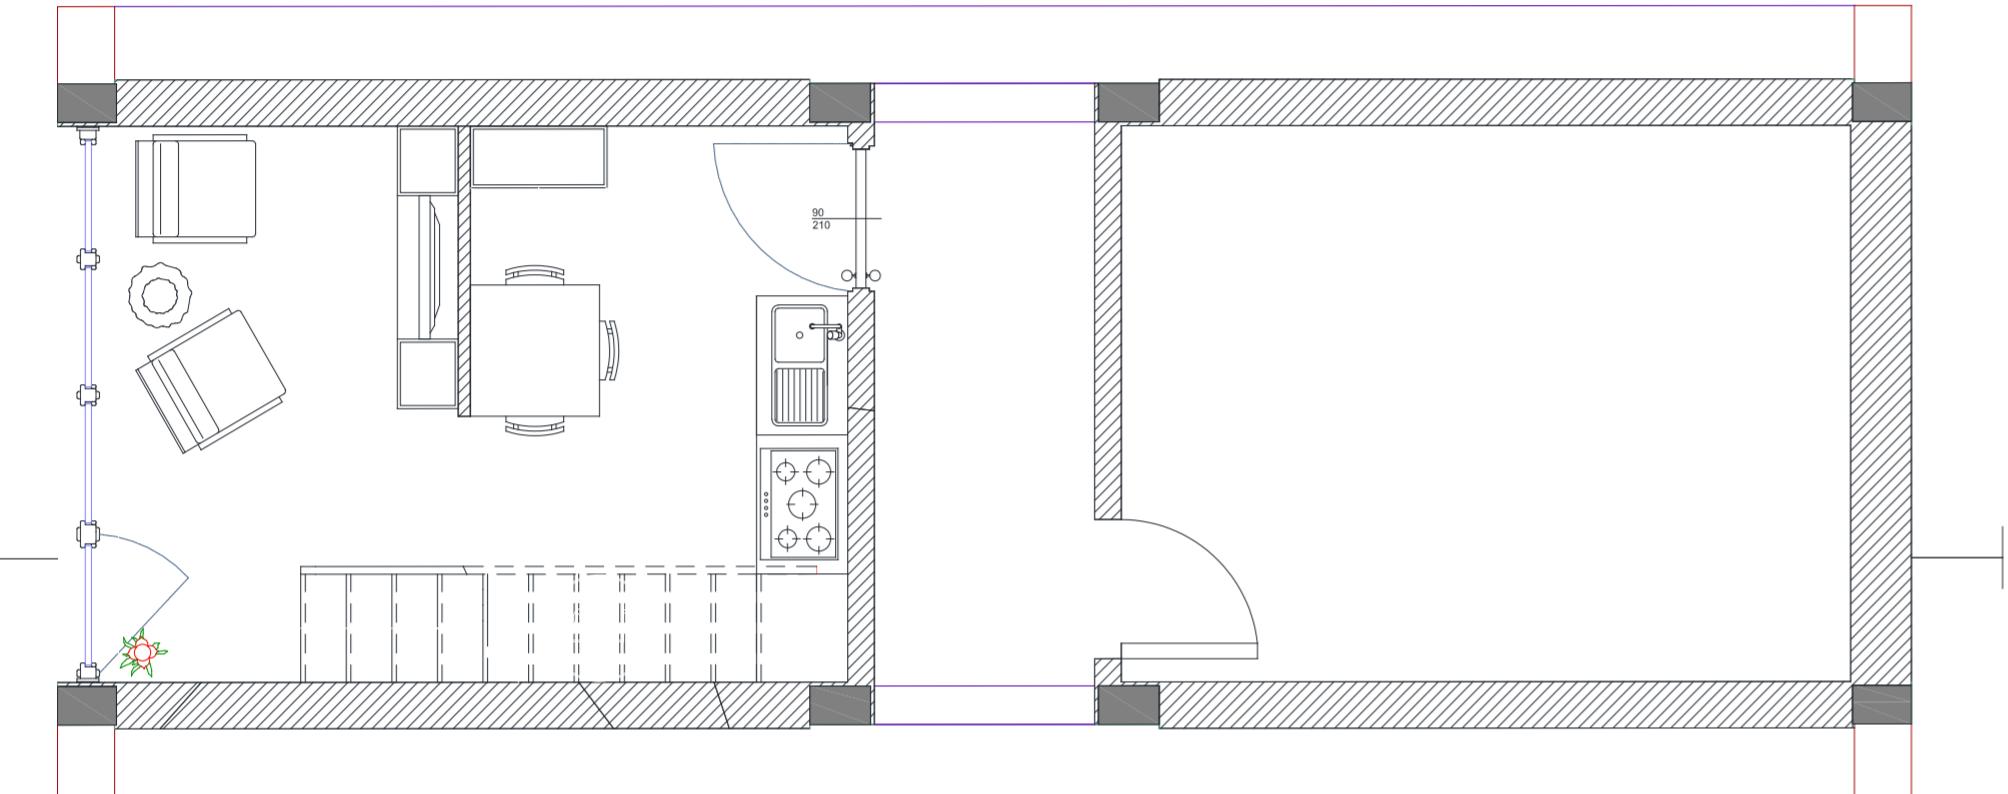


### CUCINA - DIMENSIONAMENTO

Il modulo cucina si adatta completamente alla parete cui è stato destinato: è realizzato su misura con un'altezza pari a 190 cm e tutte le dotazioni principali. Nella zona superiore del modulo frigo è stata prevista una scaffalatura a vista per evitare di venire incontro a problemi di movimento data la vicinanza con la rampa delle scale. In questo modo è divenuto possibile sfruttare anche le zone meno accessibili dell'ambiente.

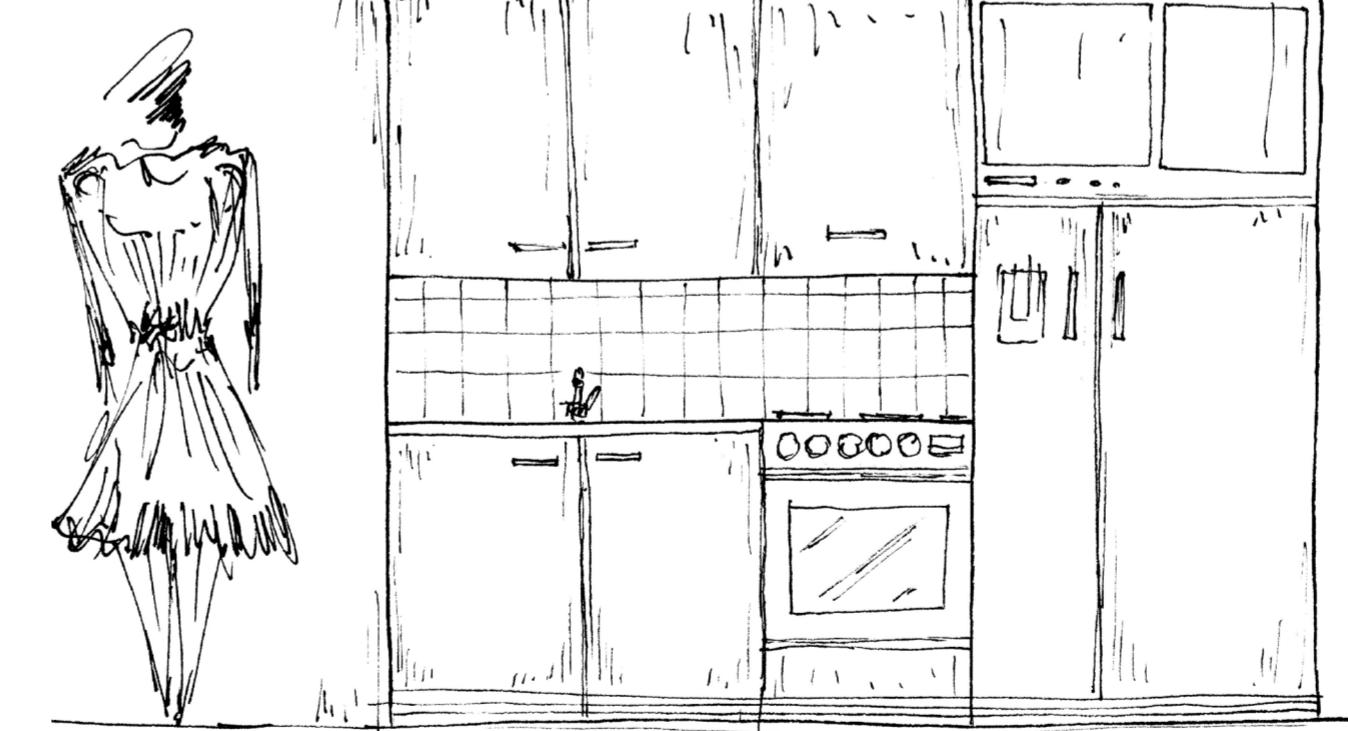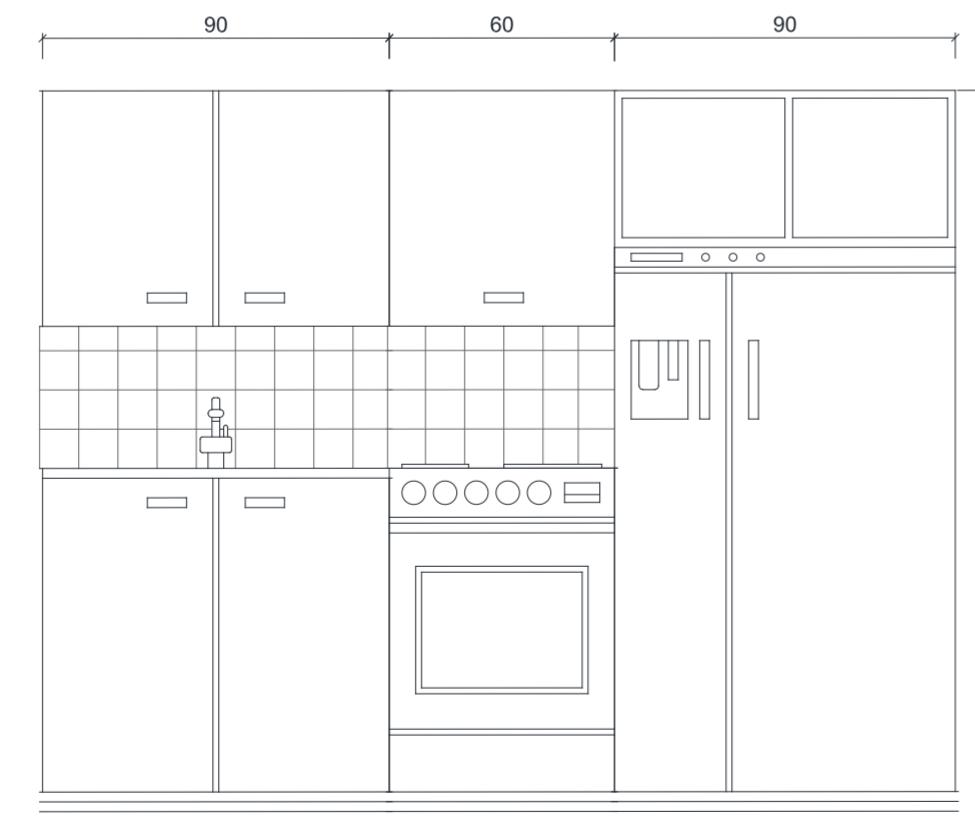


### I CONTENUTI

Gli elementi caratterizzanti di questo progetto riguardano la parte tecnica, ovvero la rappresentazione planimetrica delle superfici, e la parte figurativa, volta a rendere in maniera più immediata le scelte e le tendenze del progetto. A questo proposito saranno utili, di conseguenza, ulteriori rappresentazioni grafiche che illustrino alcuni dettagli e peculiarità degli interni. Fattore di rilevanza in questo senso sono anche gli arredi: verranno dedicati alcuni focus sugli elementi più rappresentativi dello stile di progetto e delle scelte compositive, grazie anche ai QR code che permettono di risalire direttamente allo shop per approfondire il prodotto e di conseguenza essere a conoscenza di tutti i particolari che lo riguardano.

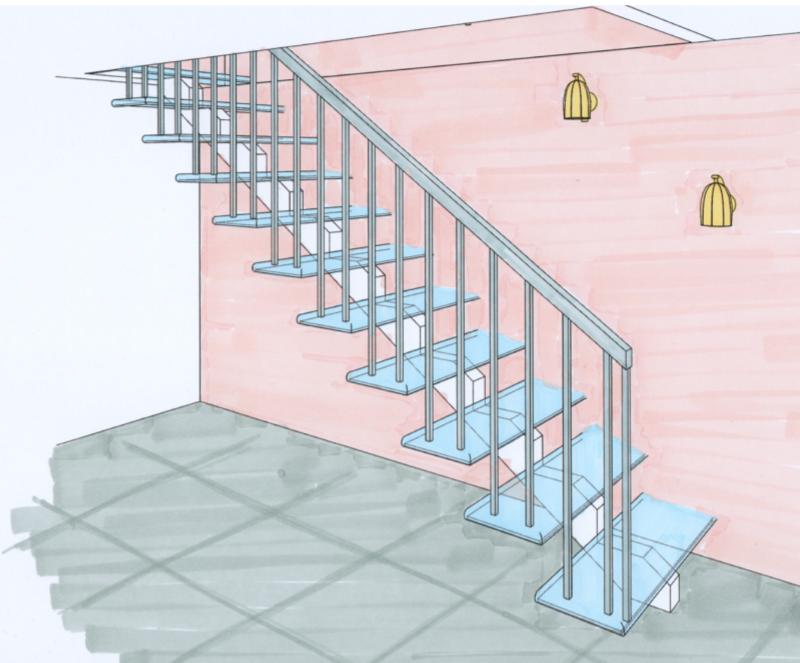

### SCALA - VISTA PROSPETTICA

Realizzata in vetro e alluminio, questa scala a trave singola lieve e coinvolgente dona sensualità all'ambiente grazie al fascino dei suoi elementi e alla leggerezza strutturale.

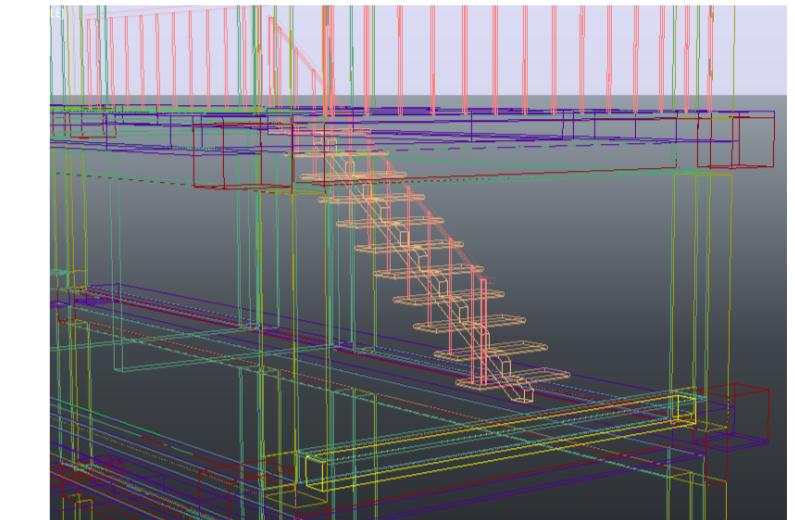

### SCALA - VISTA TRIDIMENSIONALE

In questa visualizzazione si può individuare la posizione della scala all'interno del complesso architettonico e pertanto è possibile comprenderne i volumi, le proporzioni e la rilevanza.

### POLTRONCINA DESIGN ELSA

Design : Delta Salotti  
Struttura : metallo cromato  
Finitura : ecopelle  
Imbottitura : memory foam





## CAMERA MATRIMONIALE - VISTA PROSPETTICA

In questo locale raccolto ma al contempo dotato di tutti i comfort per il riposo e il ristoro si trovano dei colori tenui e rilassanti, che in accordo con l'arredamento e i materiali conferiscono all'ambiente quella nota di tranquillità irrinunciabile per la cura di sé e del proprio partner. Una grande e luminosa vetrata con accesso sulla loggia completa l'ambiente.

## BAGNO

In questo locale dotato di doppio lavabo (visible in basso) e grande doccia rettangolare è possibile prendersi cura del proprio corpo in totale relax e senza rinunciare al comfort di una camera d'albergo. Vi è inoltre un mobile contenitore e uno specchio con luci al neon. Trovandosi a metà tra la camera padronale e quella singola, ed essendo provvista di spazio a sufficienza, rappresenta un incontro perfetto tra efficienza e utilità.




Tipologia : lavabo da appoggio tondo  
Materiale : ceramica smaltata bianca  
Finitura : bianco-opaca;  
Misure: H = 13 cm, diam. 43 cm  
Codice prodotto: 536991.26



## DIMENSIONAMENTO DI UN OGGETTO - SCAFFALE

Scaffale dalle forme essenziali e geometriche, che unisce la versatilità delle sue molteplici configurazioni alla purezza delle forme e dei colori. È composto da più pannelli assemblati fra loro in una combinazione di elementi ortogonali che vanno a costituire la struttura di appoggio.

Il materiale costitutente, la finitura e lo spessore dei pannelli consente allo scaffale di sostenere anche dei carichi notevoli, grazie anche la robustezza del sistema di ancoraggio a parete. Nel progetto della suite è previsto nella zona living sovrastante il televisore.


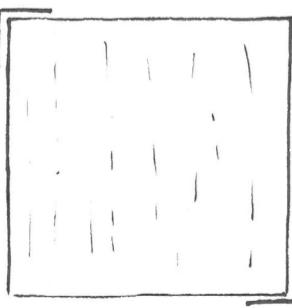


## MATERIALI



Truciolare, fibra di legno, lacca acrilica, cartone a nido d'ape ( 100% riciclato ), bordo in materiale plastico.

Larghezza totale : 105 cm  
Altezza totale : 65 cm  
Profondità : 35 cm  
Peso : 3.6 kg

MISURE OGGETTO  
SCALA 1:10

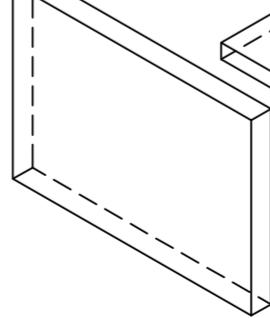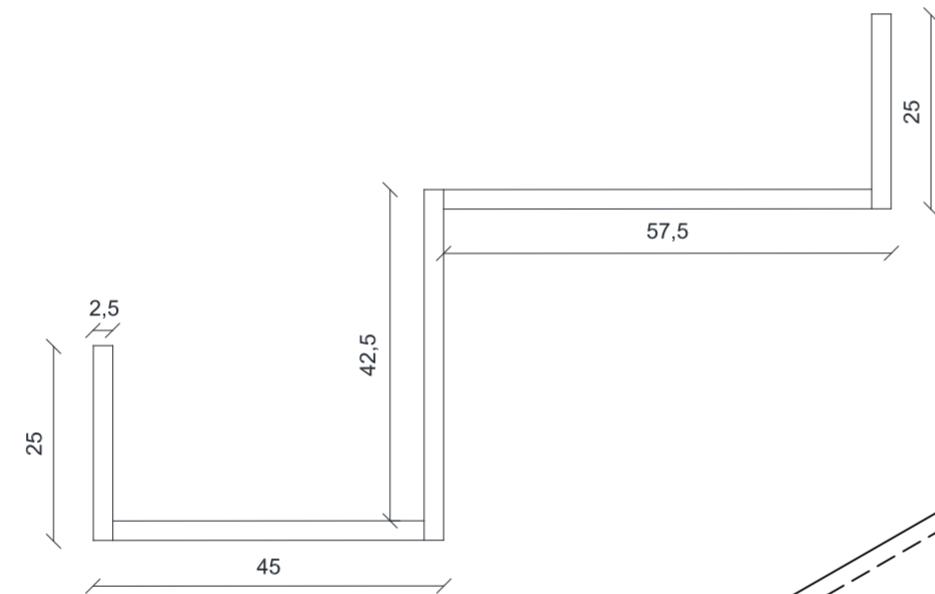


ESPLOSO ASSONOMETRICO

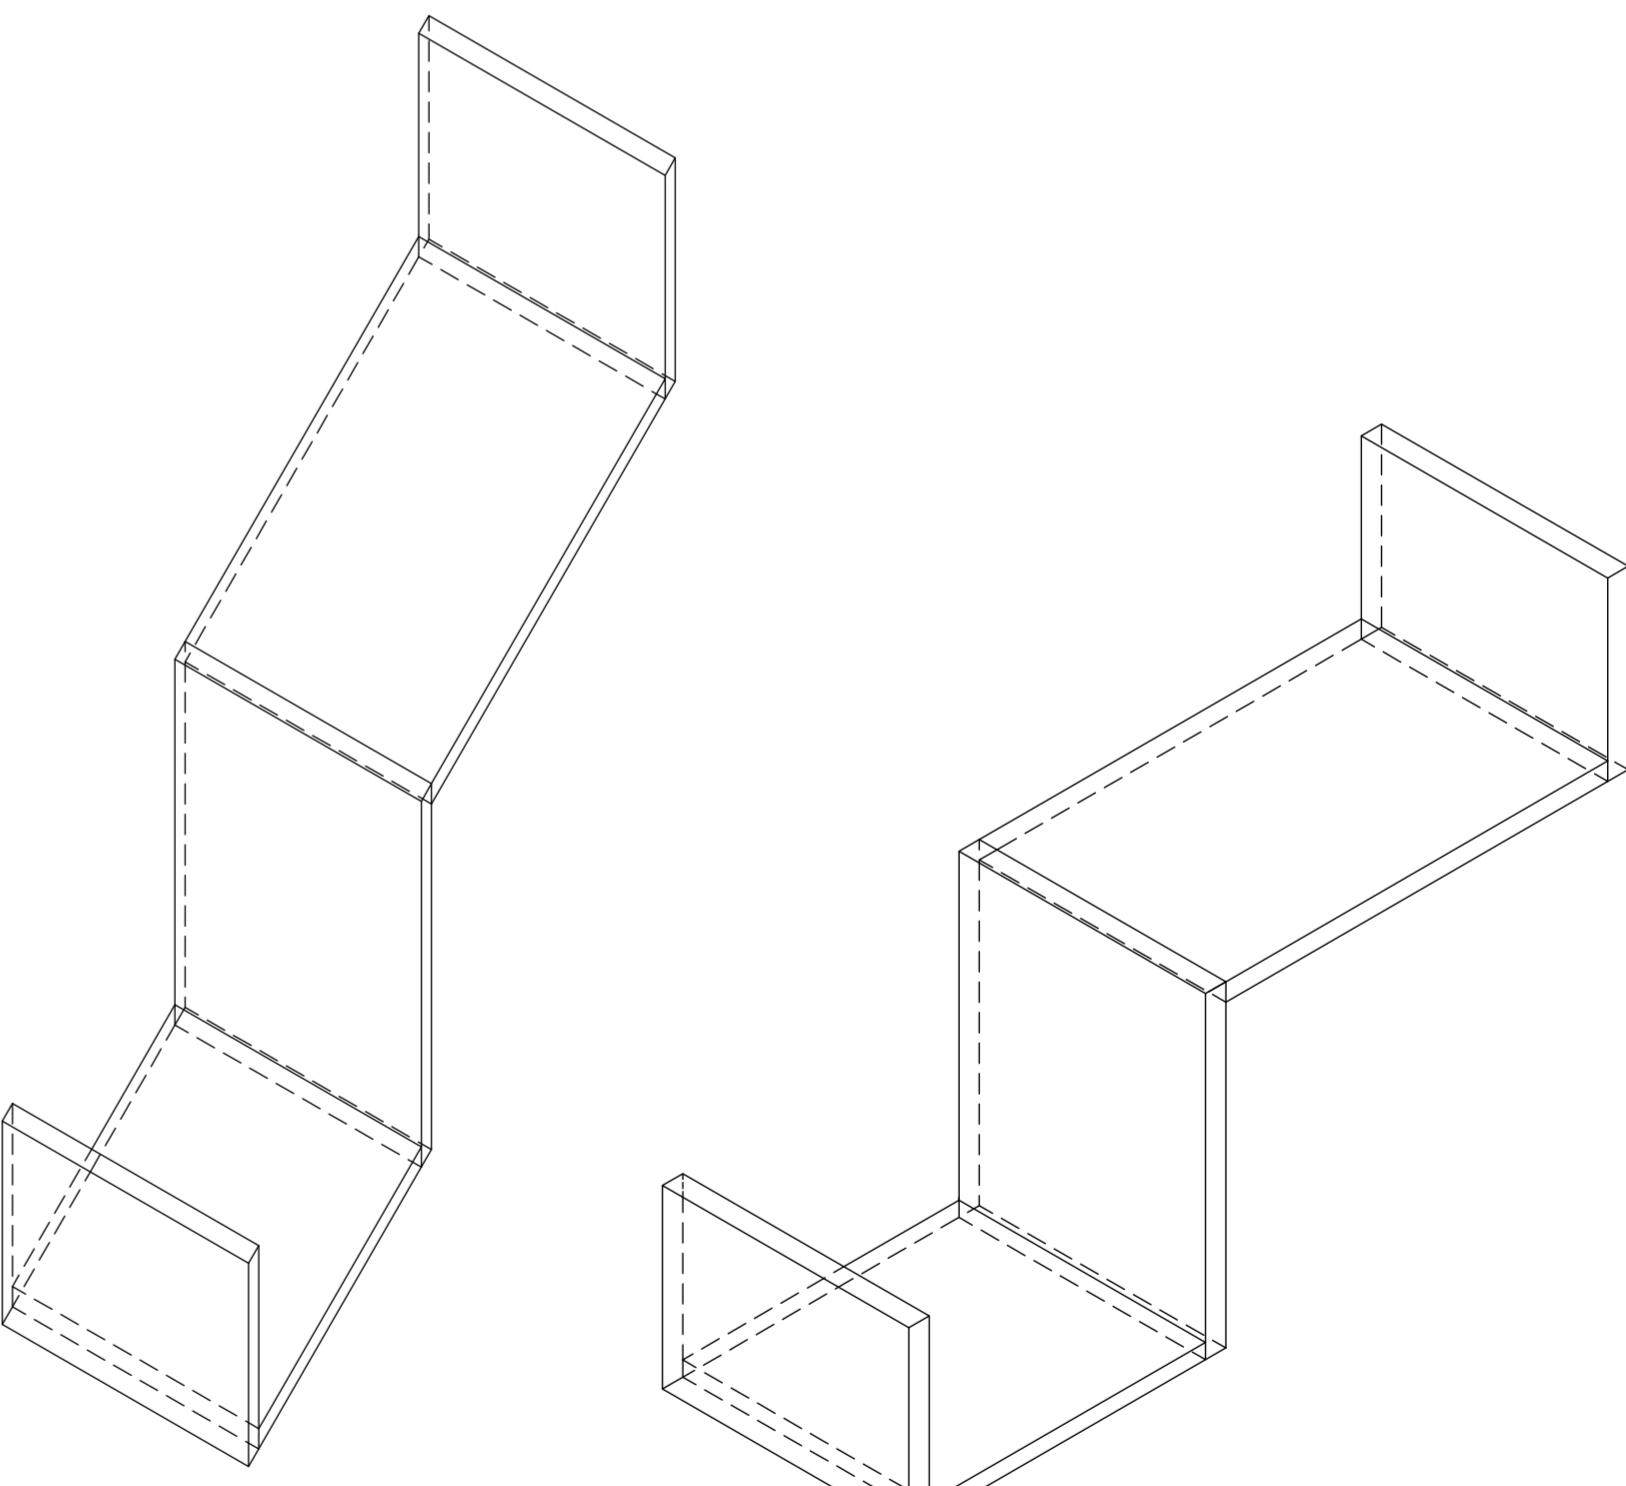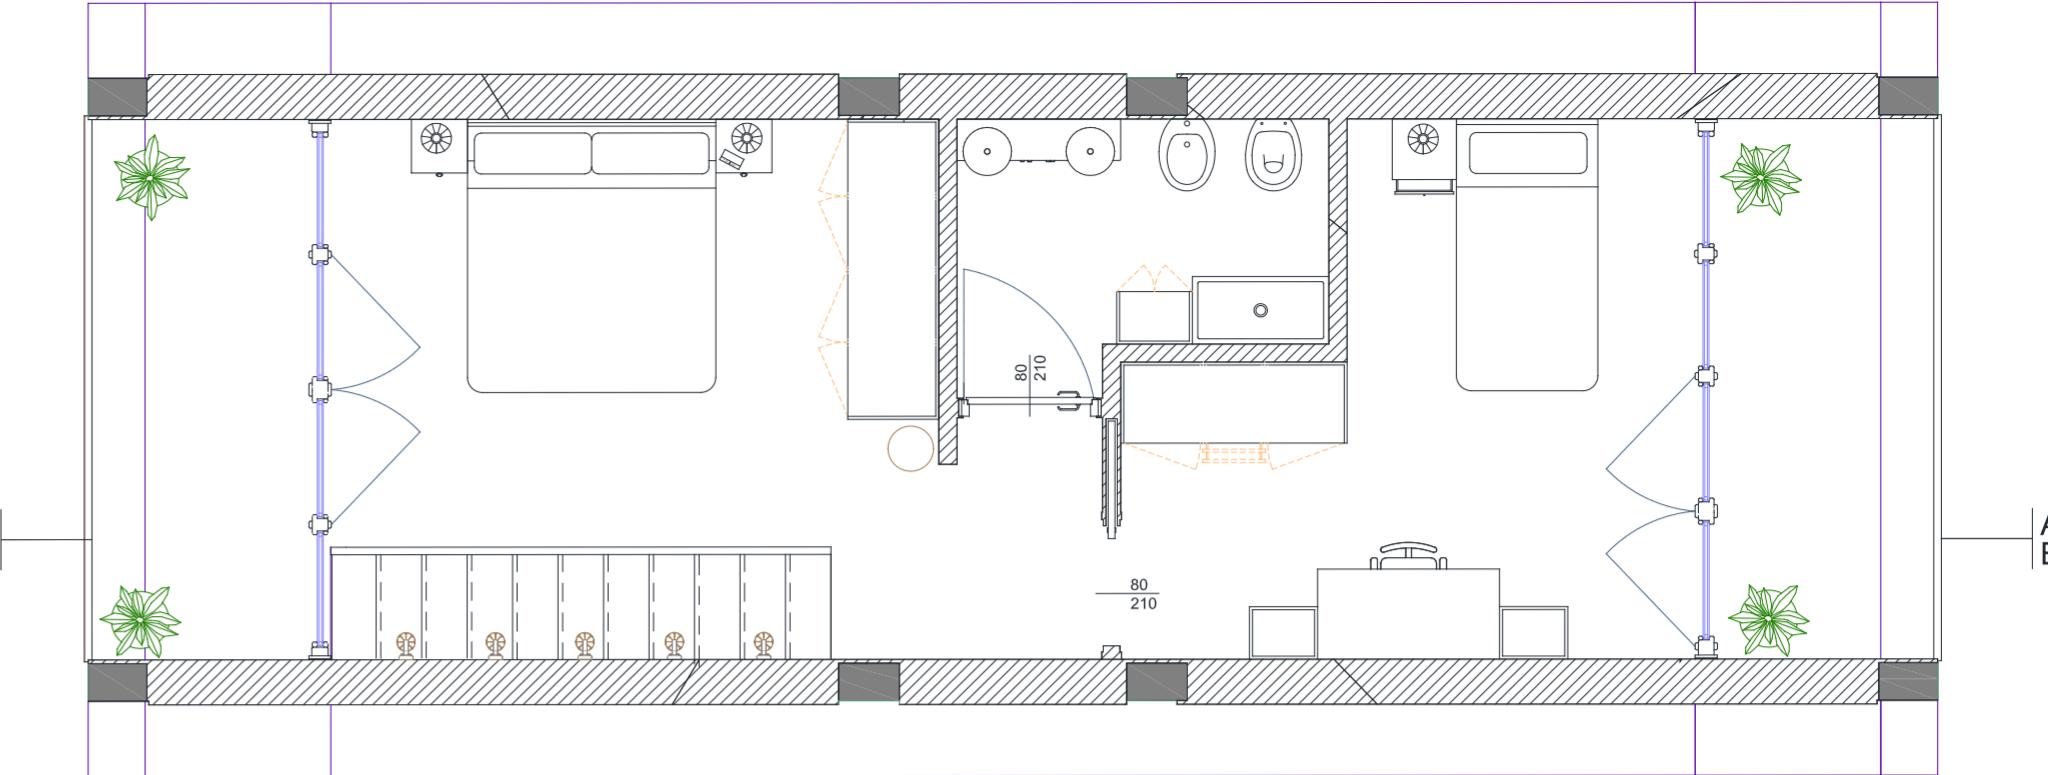

ASSONOMETRIA MILITARE

ASSONOMETRIA ISOMETRICA

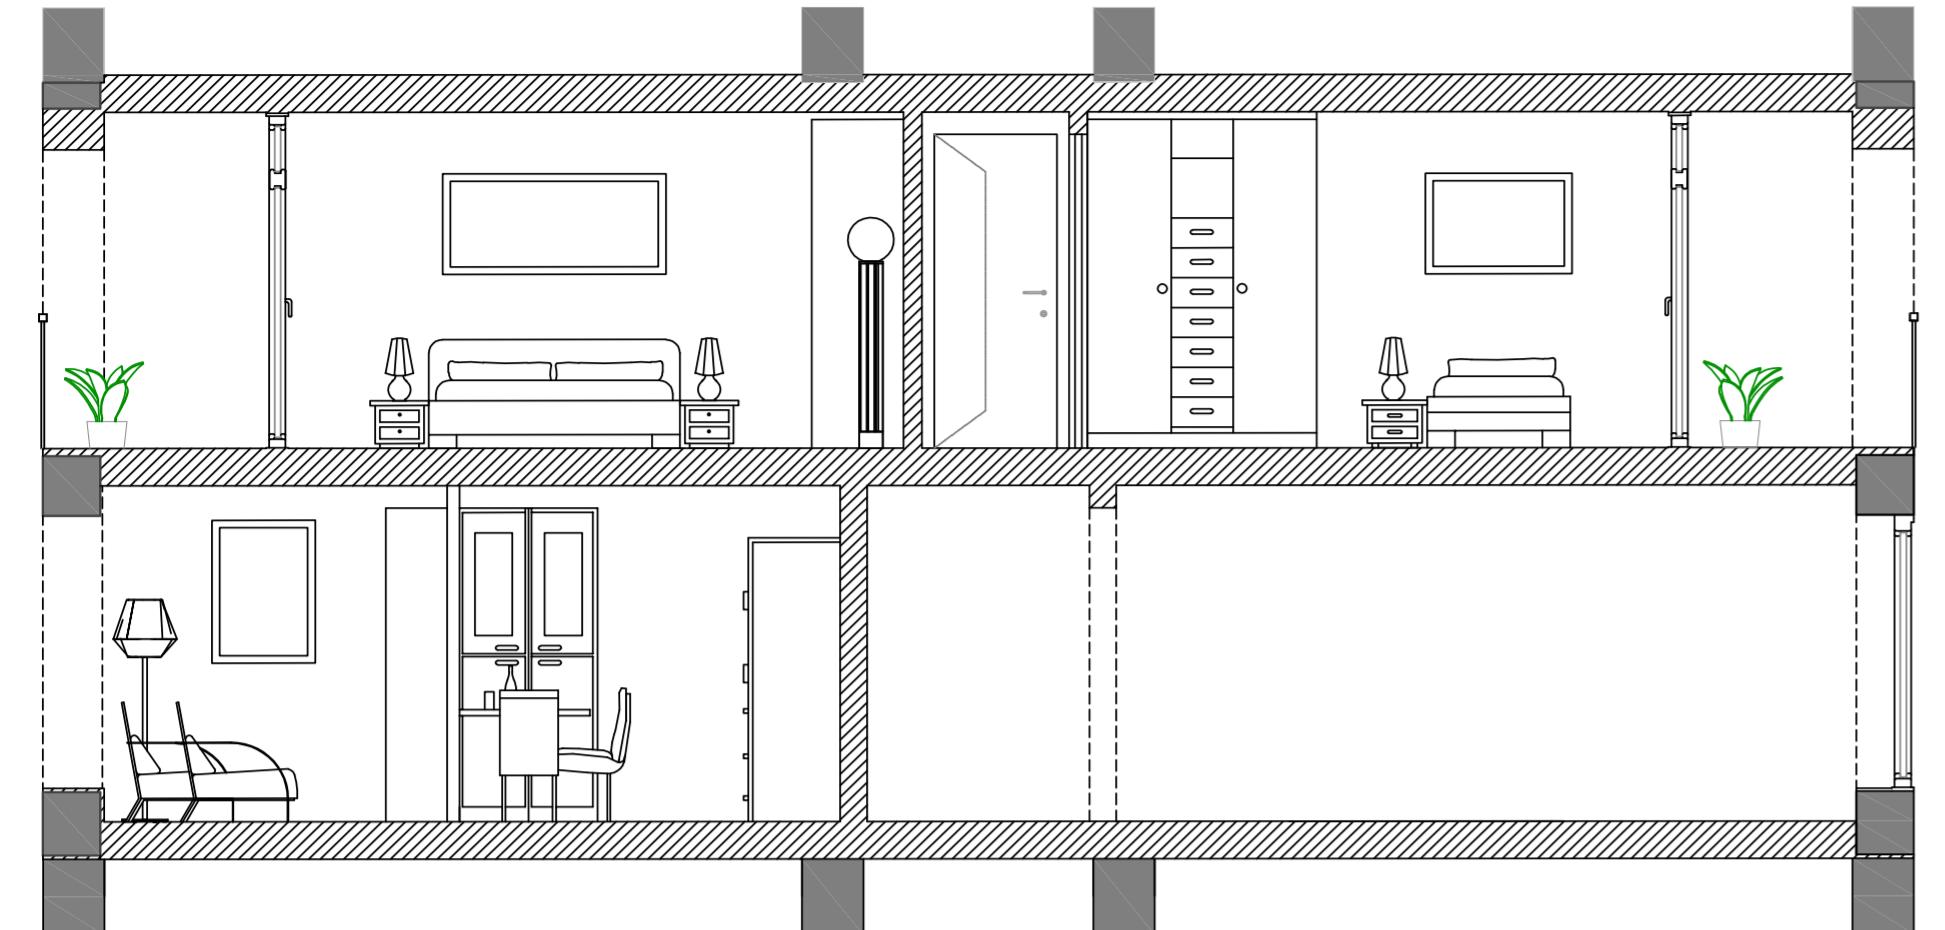

LA DRACENA

Durante la realizzazione di questa suite si è tenuto in considerazione anche l'aspetto "green" della progettazione. Pur trovandosi in un contesto urbano, è sempre possibile limitare la circolazione di sostanze dannose per l'organismo umano, a cominciare da quelle tossiche. Negli ambienti interni ed esterni sono state incluse, a questo proposito, alcuni esemplari di Dracena. Questa pianta ha la caratteristica di depurare l'aria degli spazi assorbendo le sostanze inquinanti che sono presenti nell'aria senza che ce ne accorgiamo: dall'anidride carbonica fino alle famigerate polveri sottili. È proprio unendo questa preziosa virtù alla loro bellezza che queste piante possono migliorare la nostra aria e quindi la nostra salute.

LAMPADA DA TERRA LIBRERIA - BLACK



Design : Folkform

Finitura : nera

Materiale : acciaio verniciato a polvere e vetro opaco, cavo tessile da 2 m con tappo shouko

Sorgente luminosa: 6W LED E27

Classe II IP20 230V

Dimensioni : L = 30 cm, H = 155 cm

Prezzo : £ 695,00 GBP



SALICE RB429-020

Applique lavorata a mano in vetro soffiato con le tecniche dei vecchi maestri vetrai di Murano.

Design : Siru Venezia

Potenza : 250V

Sorgente luminosa IP20 1E14 max 60W ~ 1E12 max 40W ~


Dimensioni : L = 12 cm, H = 22 cm, P = 18 cm




## LE SEZIONI

Gli elementi caratterizzanti di questo progetto riguardano la parte tecnica, ovvero la rappresentazione planimetrica delle superfici, e la parte figurativa, volta a rendere in maniera più immediata le scelte e le tendenze del progetto. A questo proposito saranno utili, di conseguenza, ulteriori rappresentazioni grafiche che illustrino alcuni dettagli e peculiarità degli interni.


SEZIONE B-B' 1:50

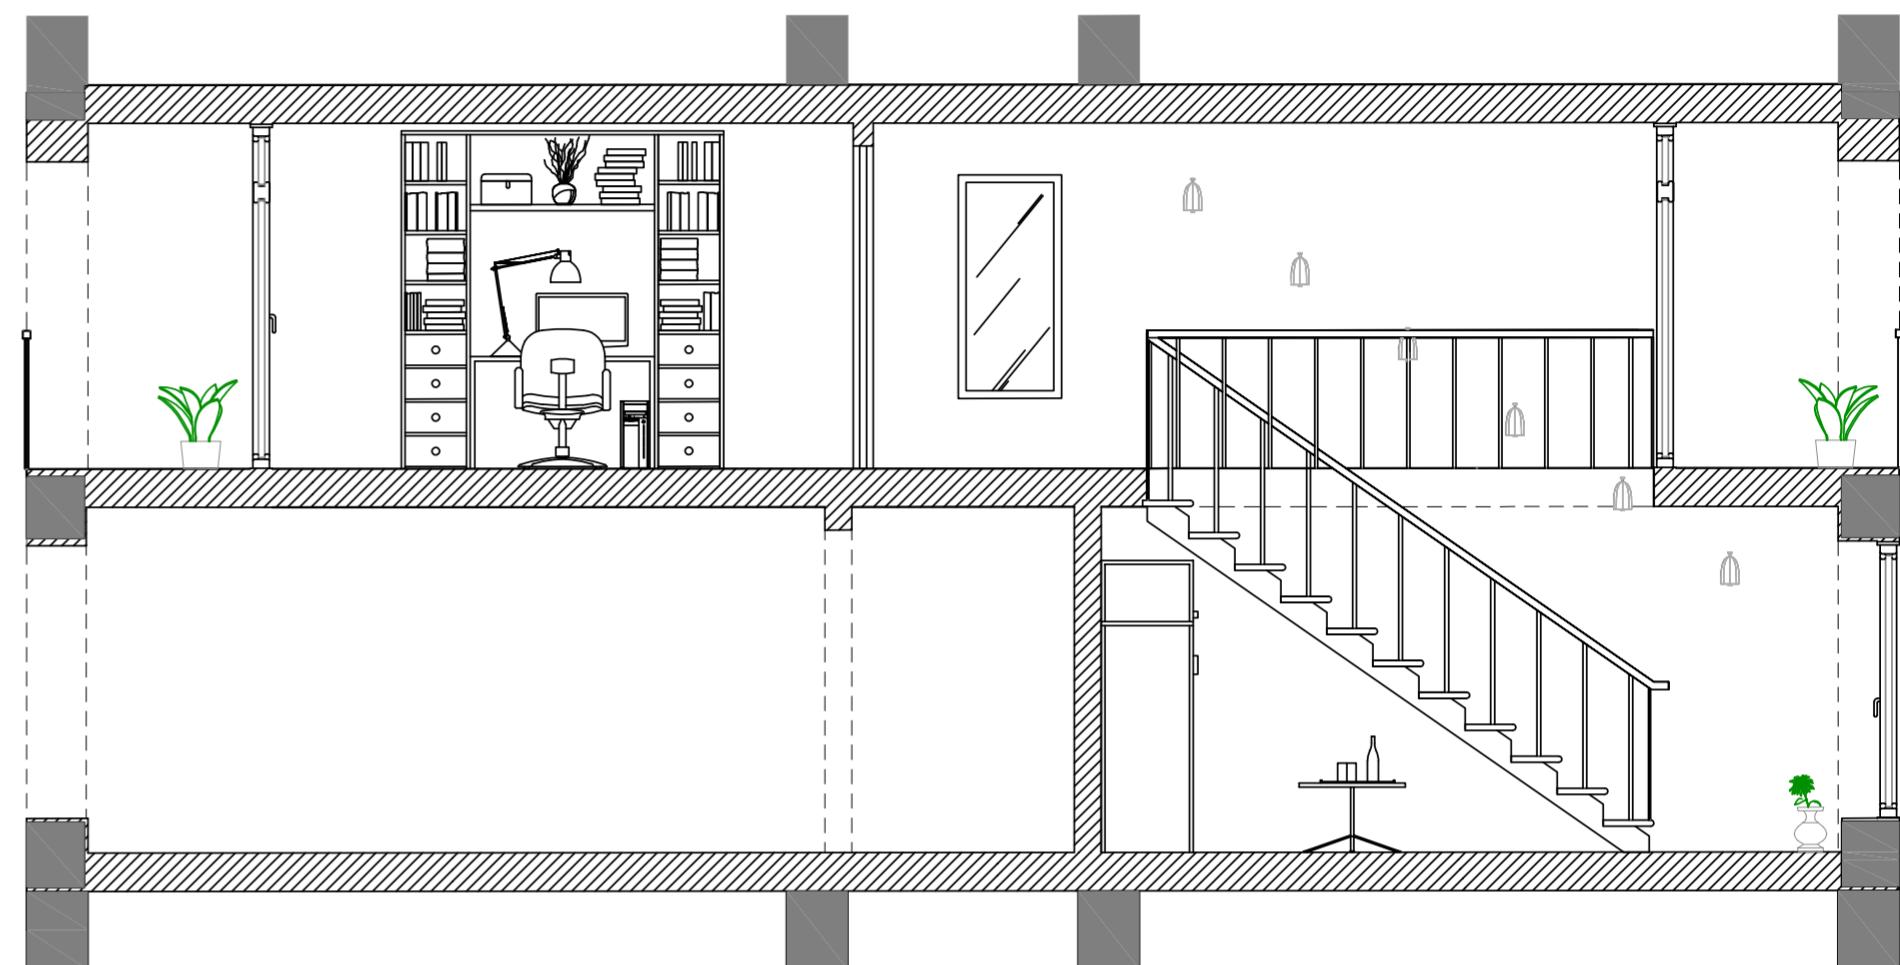


PROSPETTO 1:50

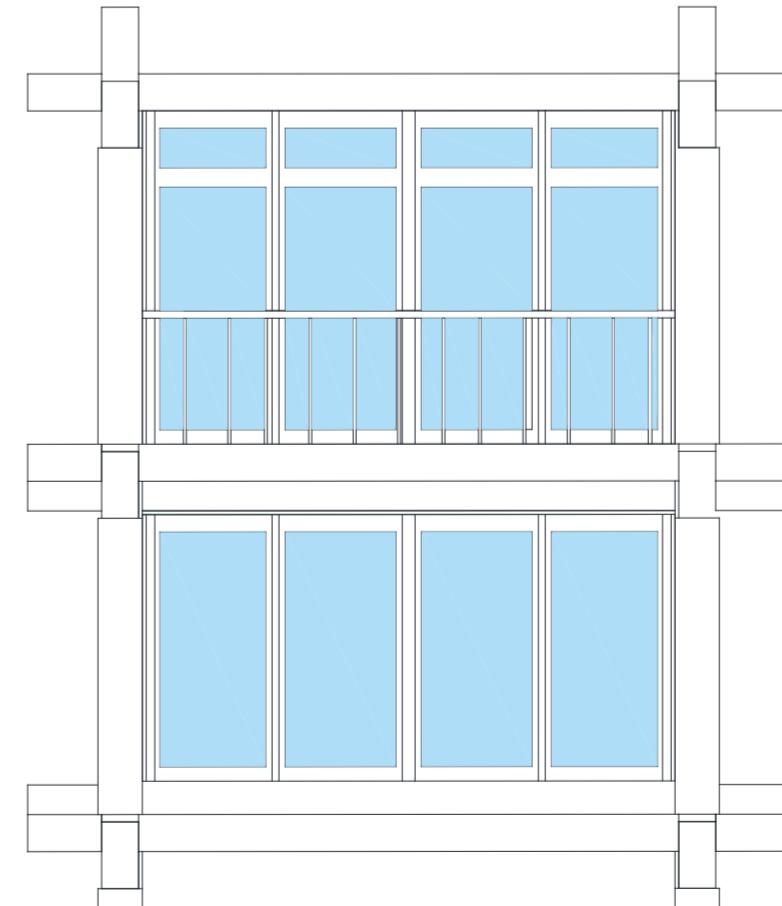



DETTAGLIO

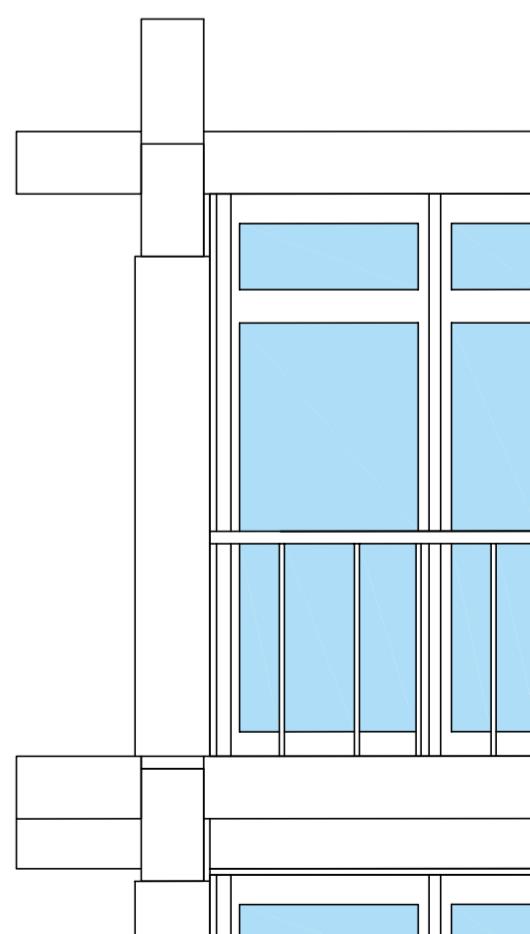




LE FINESTRE - LIVELLO A - 1:20

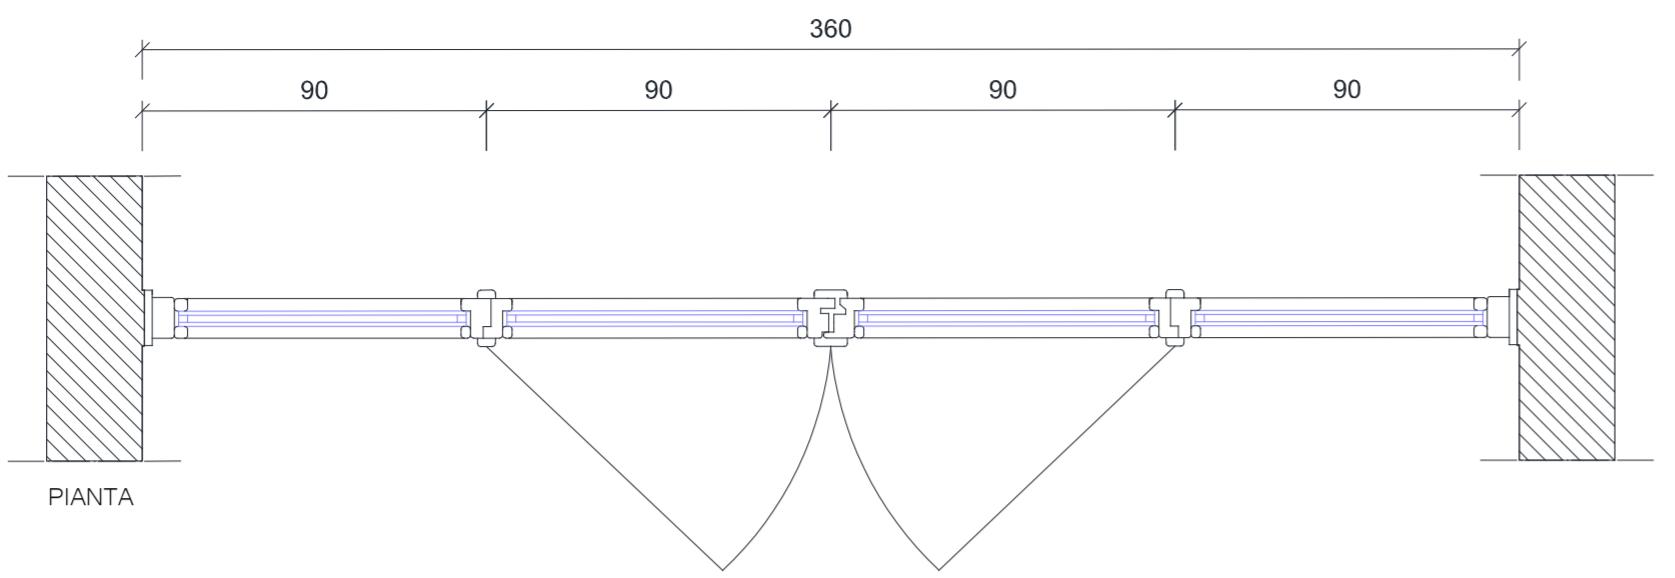

LIVELLO AB - 1:20

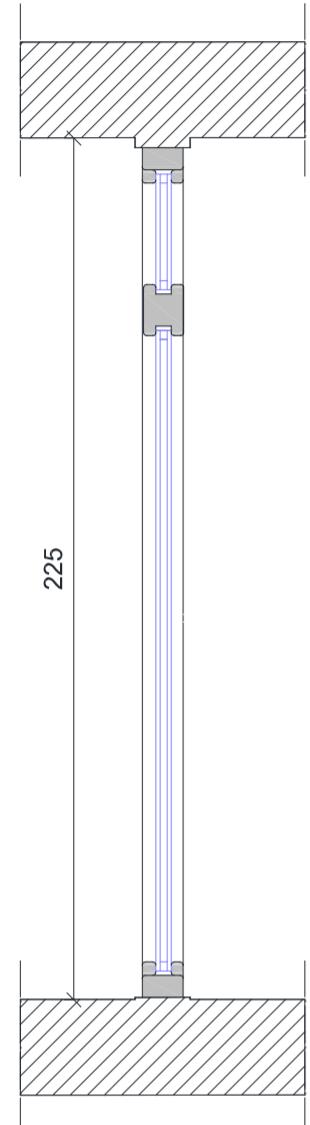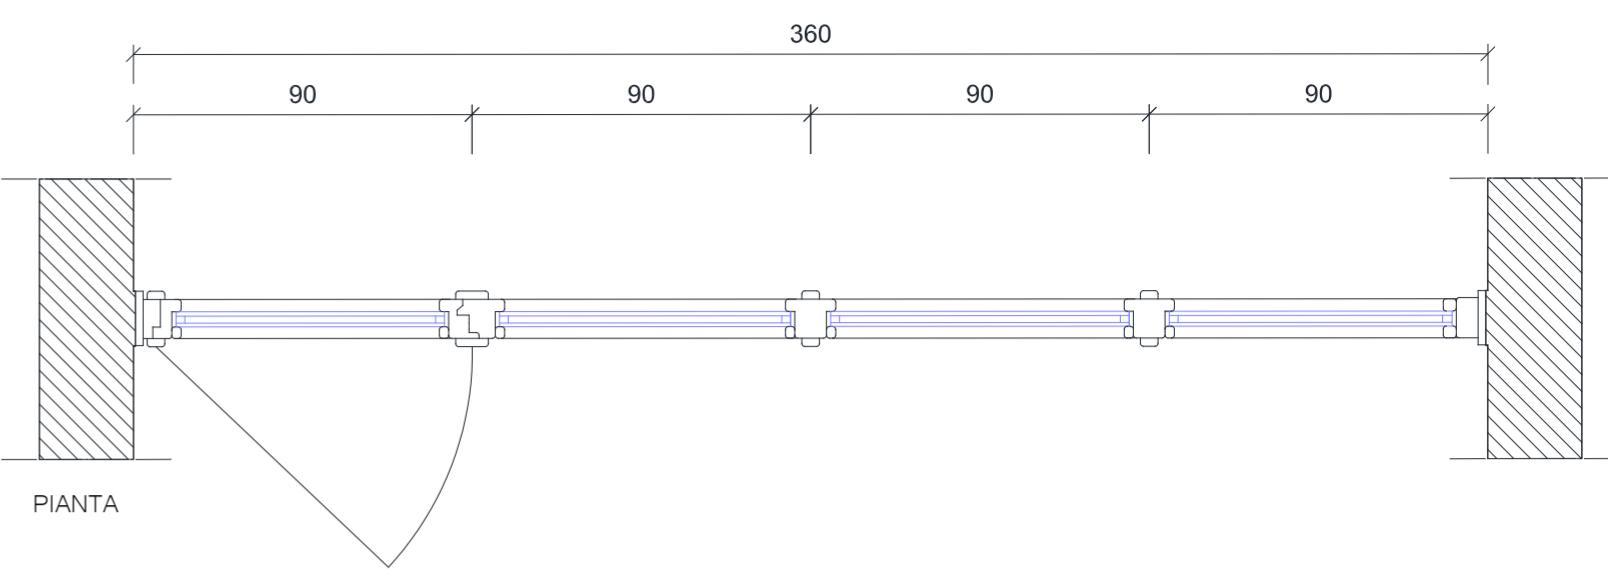

SEZIONE

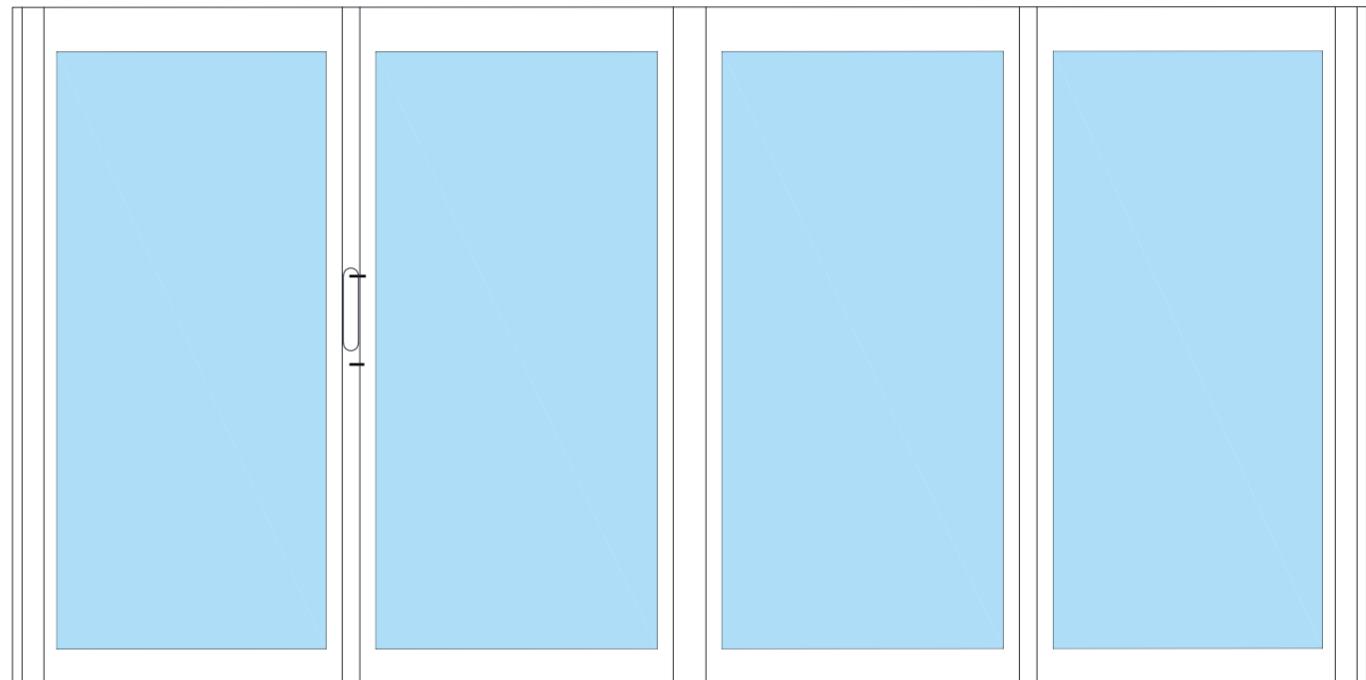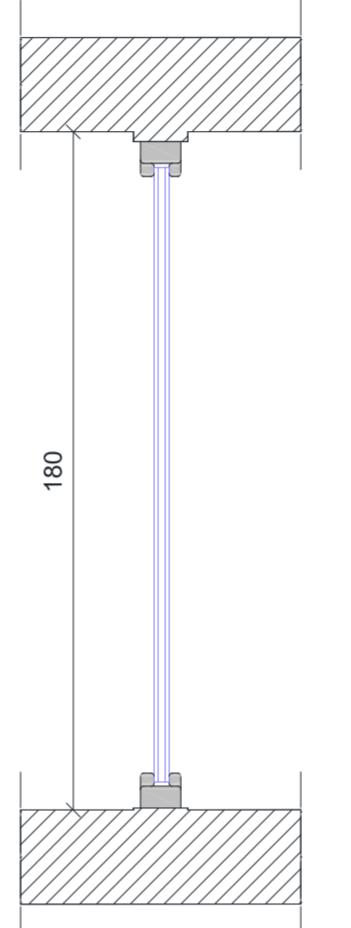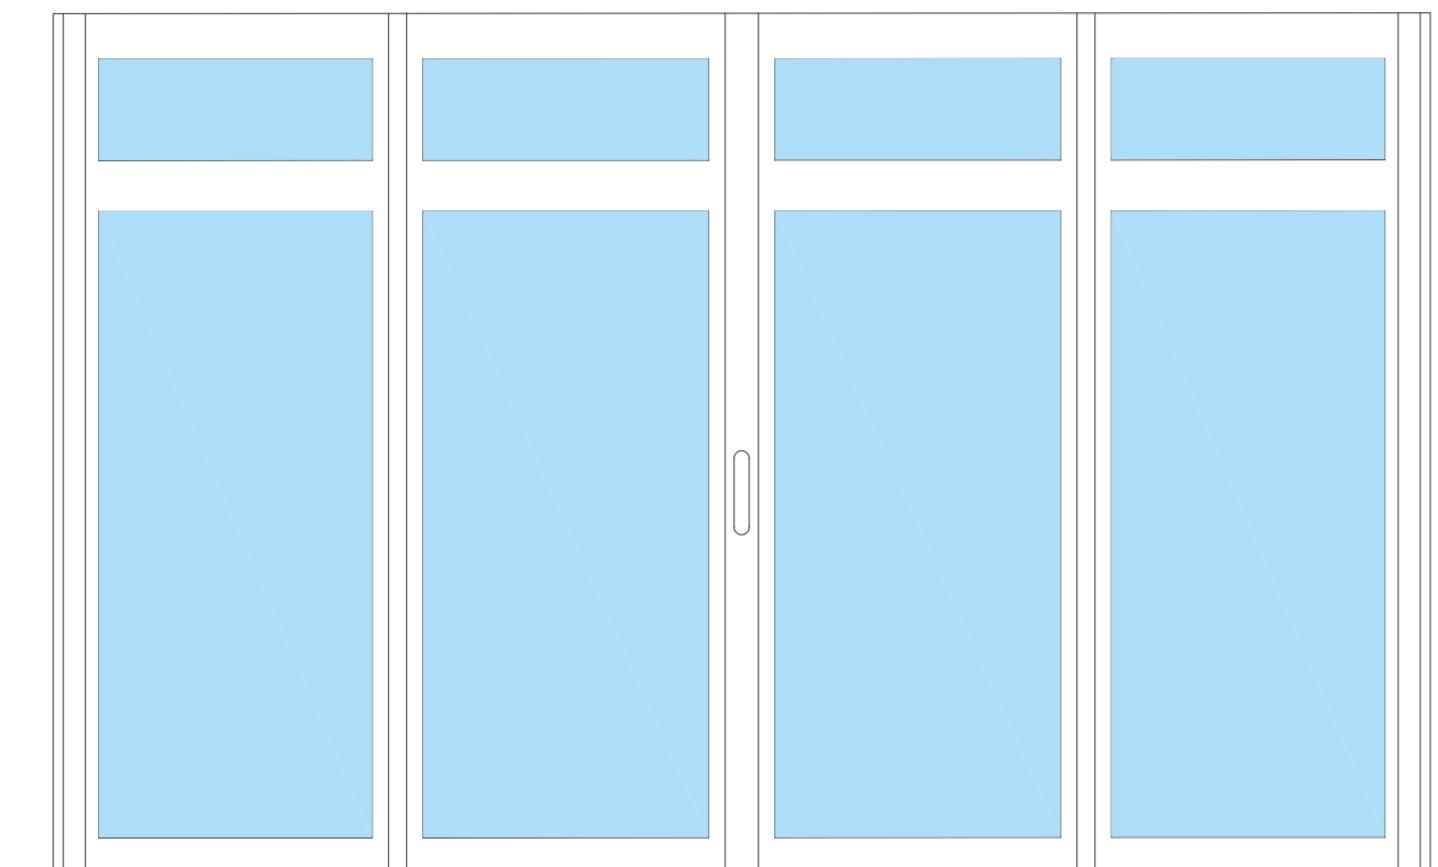

#### INFISSI IN ALLUMINIO

Il progetto prevede l'installazione di n. 3 infissi della larghezza di 360 cm lungo 3 pareti della suite. Uno dei principali punti di forza dell'infisso in alluminio è la durata nel tempo : questo vantaggio è dovuto all'estrema resistenza dell'alluminio all'ossidazione e alla sua resistenza meccanica. Un altro vantaggio conseguente è la possibilità di avere finestre molto sottili, con un design molto snello e pulito. E' possibile realizzare le finestre cosiddette "tutto-vetro" senza nessun tipo di problema meccanico. Finestre luminose e resistenti.

