

breezy suite

Un piccolo angolo di convivialità _

Breezy è una suite strutturata su due piani che si presenta sin dall'ingresso come un ambiente accogliente e raffinato, predisposto ad accogliere giovani coppie che ricercano un gusto moderno senza rinunciare alla semplicità.


Al primo piano si trova un open space con cucina e tavolo da pranzo, da cui si accede, salendo le scale, alla zona più privata della suite: il salottino, i servizi igienici e infine la camera da letto.

Entrambi i lati del secondo piano danno accesso ad un terrazzino da cui godere della vista sulla splendide colline circostanti. Nota positiva dell'appartamento è infatti la grande disponibilità di luce naturale conferita dalle tre facciate a vetro, pronte ad accogliere luce durante tutto il giorno.

La disposizione degli ambienti è stata pensata per distinguere la zona semipubblica dalla zona più privata. Il piano inferiore si presta infatti ad accogliere ospiti, mentre di sopra il flusso che attraversa li spazi riconduce ad un utilizzo più intimo dell'area.

L'orientamento della scalinata, volto a stupire gli ospiti con l'aprirsi della visione sulla suite, ha consentito di sfruttare il sottoscala per inserire il piano della cucina, insieme ai relativi scaffali utili a contenere l'essenziale.

All'ingresso si trova una consolle per poggiare i propri beni e uno specchio retroilluminato, che crea una particolare atmosfera la sera.

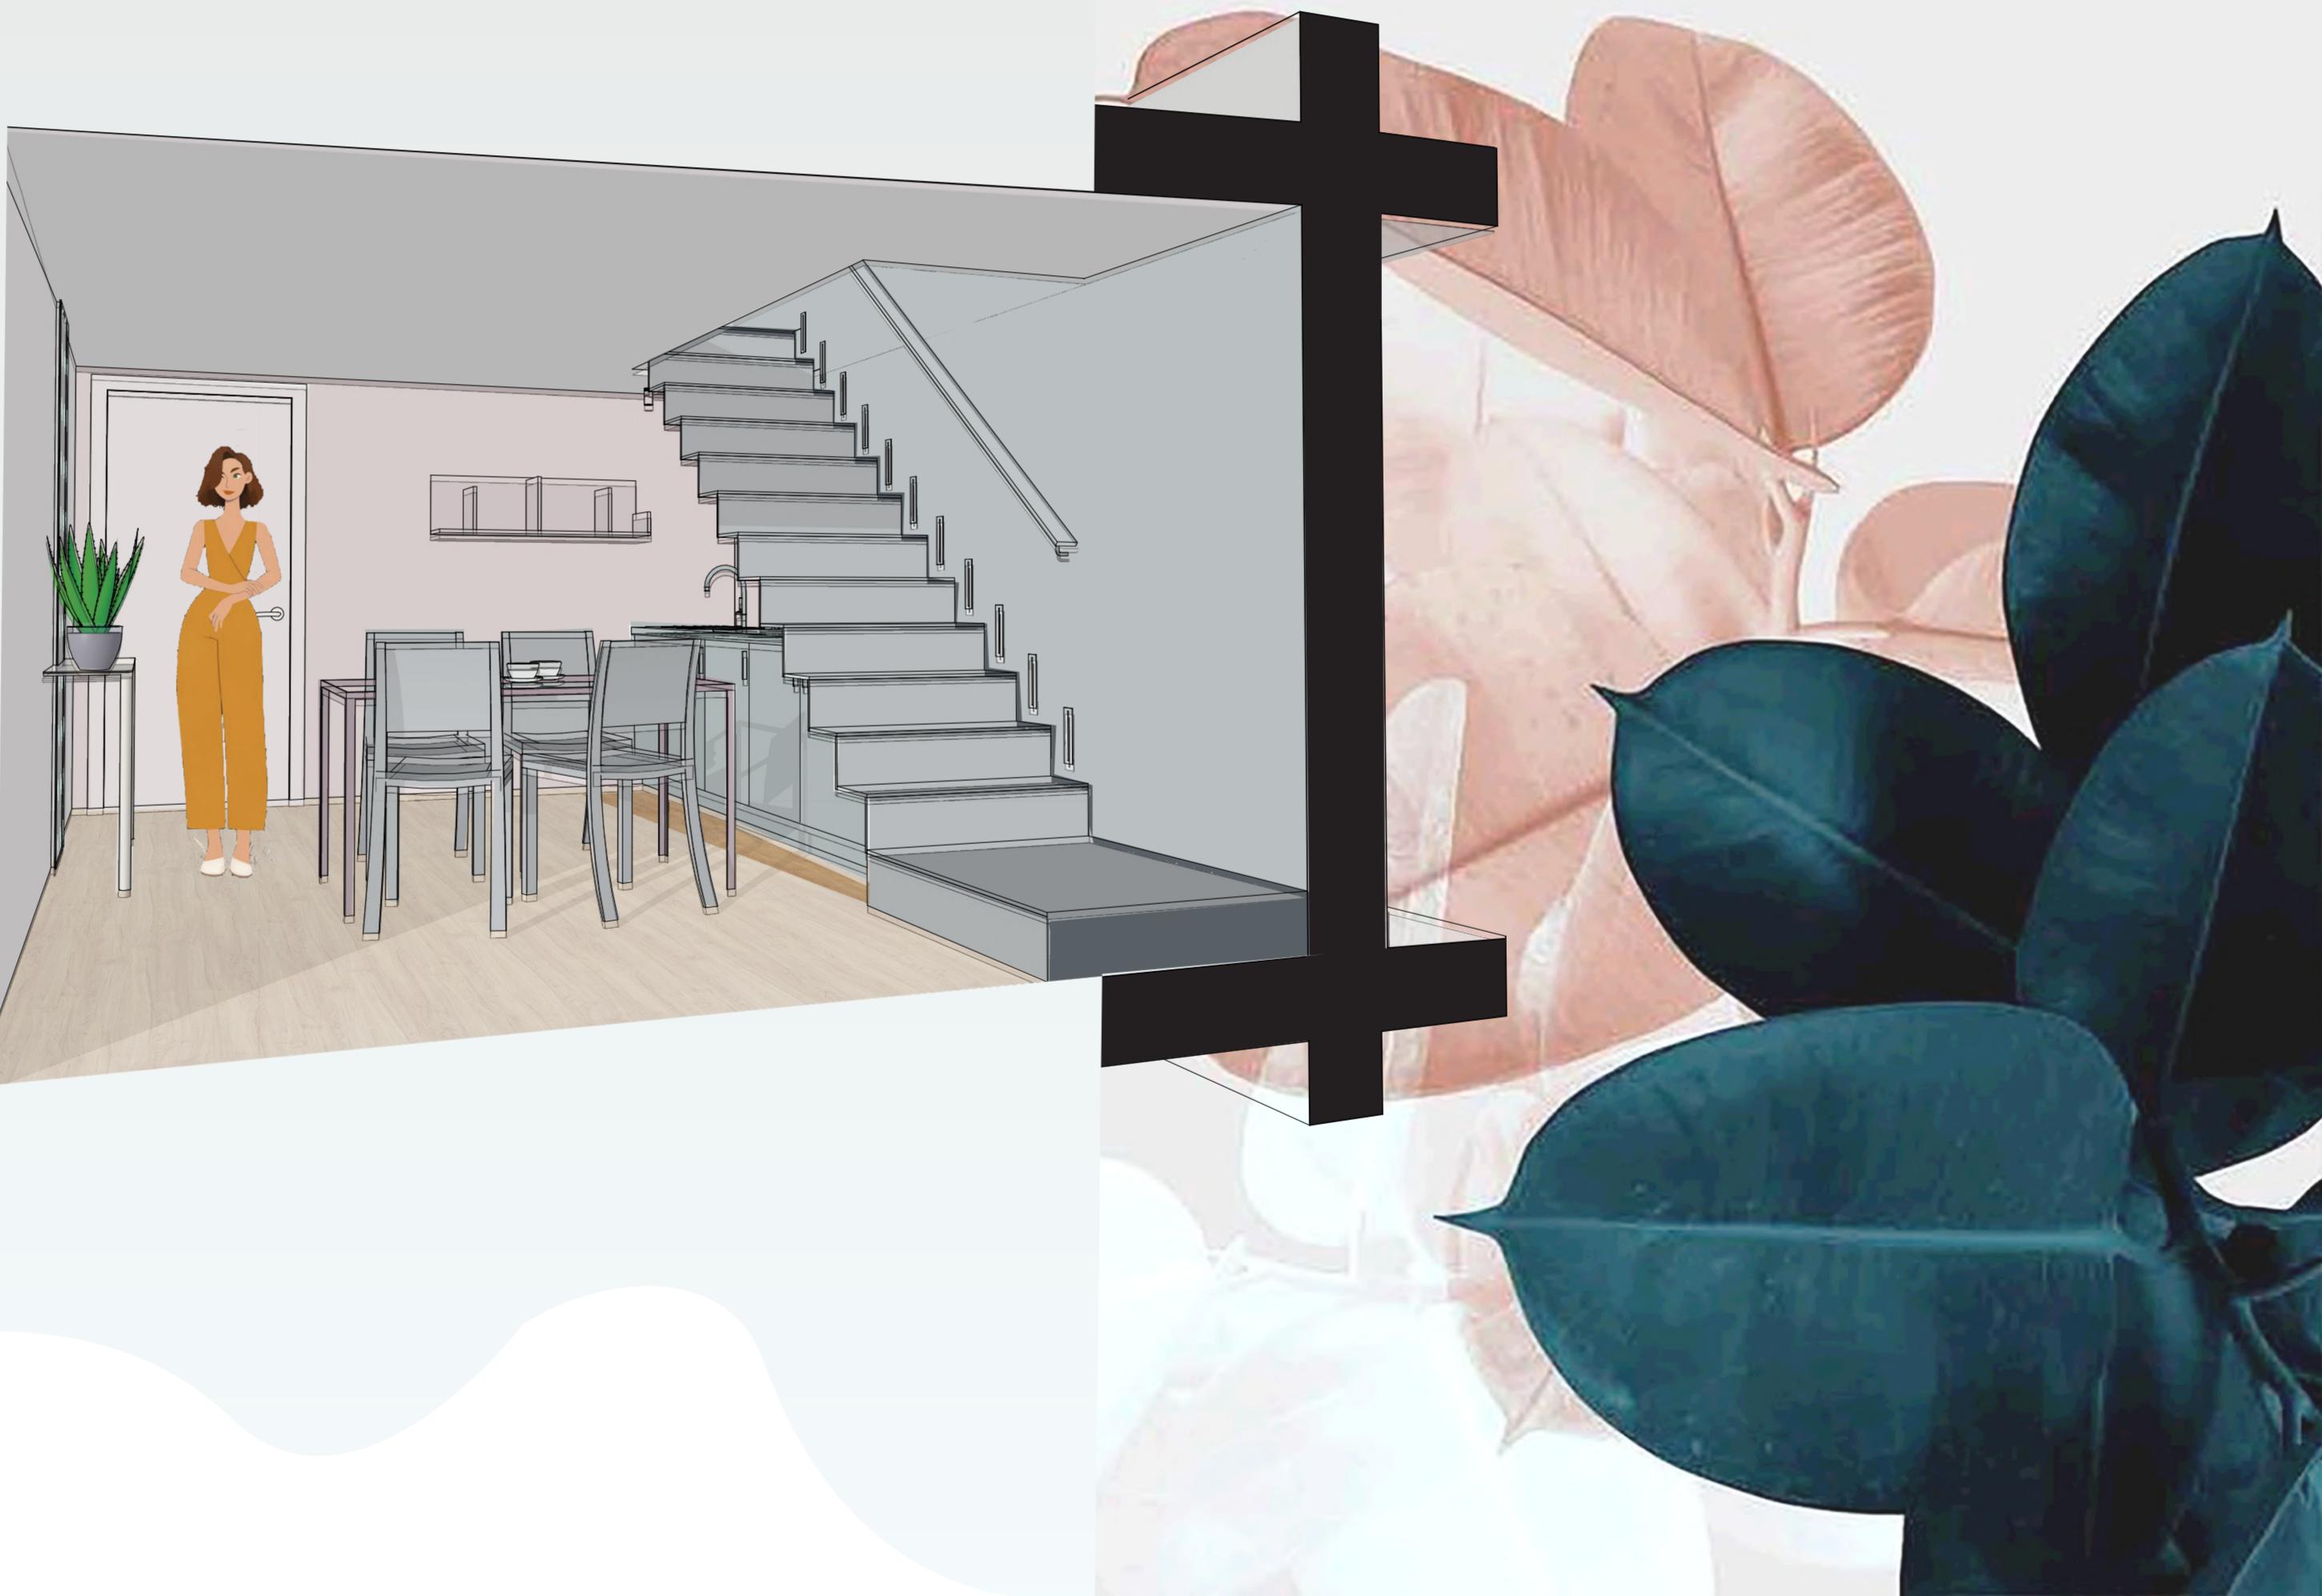

breezy suite

Connesso, sconnesso _


Breezy continua al piano superiore in uno spazio aperto e connesso in tutte le direzioni. La ricerca di uno flusso continuo in tutta la sua lunghezza ha allontanato l'idea di porte e pareti, che occludono la percezione dello spazio. La separazione tra gli ambienti è infatti conferita esclusivamente dai cambi di materiale e di tonalità, nel tentativo di avvezzare i fruitori ad una visione sempre più aperta dell'abitare la propria casa e gli spazi.

Dal soggiorno si passa necessariamente attraverso il "bagno" o, per meglio dire, l'ambiente riservato alla cura e pulizia del corpo, comunemente percepito come un invalicabile momento privato.

Il soggiorno, dotato di tv e di divano letto che all'occorrenza può essere estratto, offre accesso alla veranda con tavolino.

Nell'area dei servizi igienici si trovano due lavandini a sospensione con specchio retroilluminato. La doccia si trova sulla parete di fronte, rivestita di ardesia e dotata di una nicchia orizzontale illuminata a led. Dietro ad essa si trova l'unico spazio chiuso della suite, il wc, cui si accede da ambi i lati attraverso delle porte scorrevoli in vetro oscurato.

La camera padronale gode di un ampio armadio, letto con testiera-comodino e una vista mozzafiato sulla baia, sia di giorno che di notte.

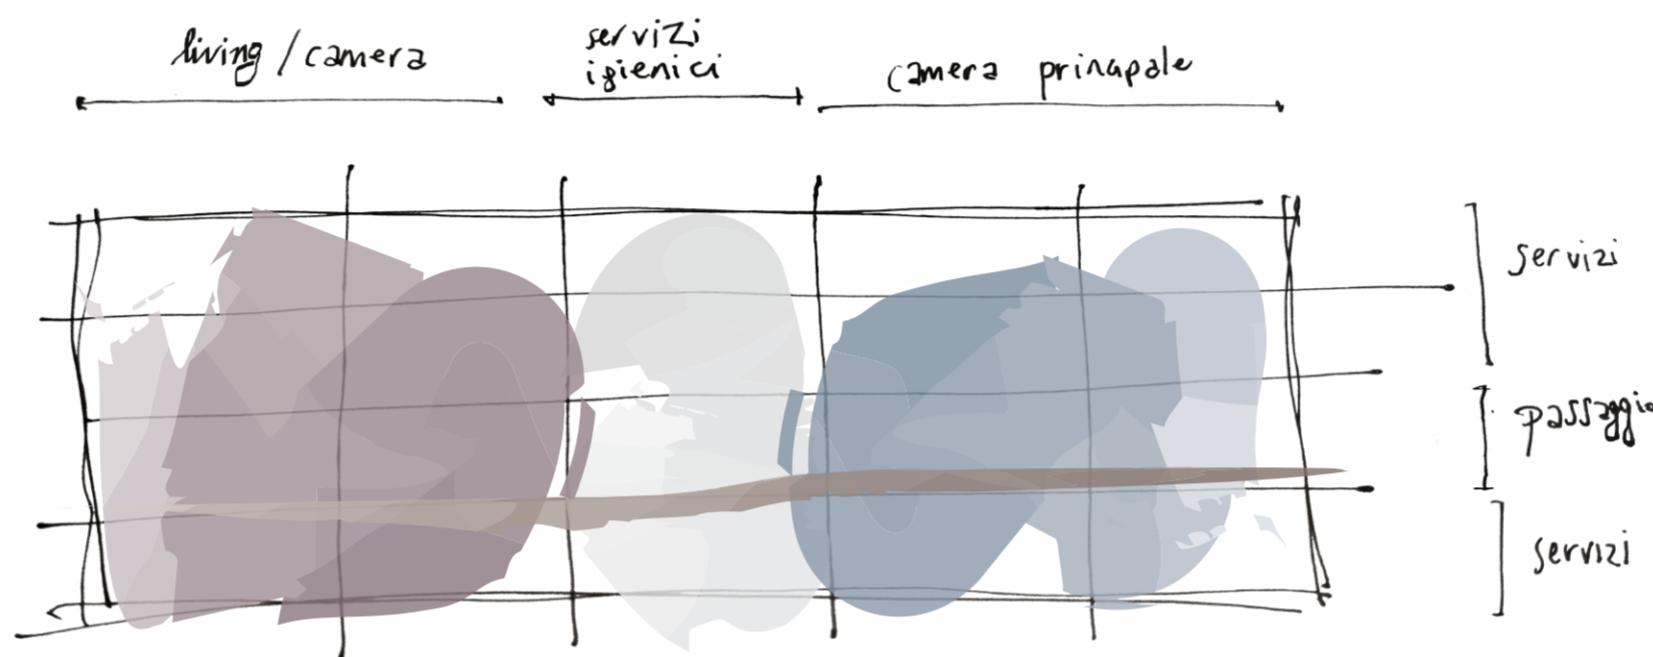


Lo schema racconta la struttura degli spazi,
punto nevralgico del progetto.



breezy suite

CAMERA
DA LETTO

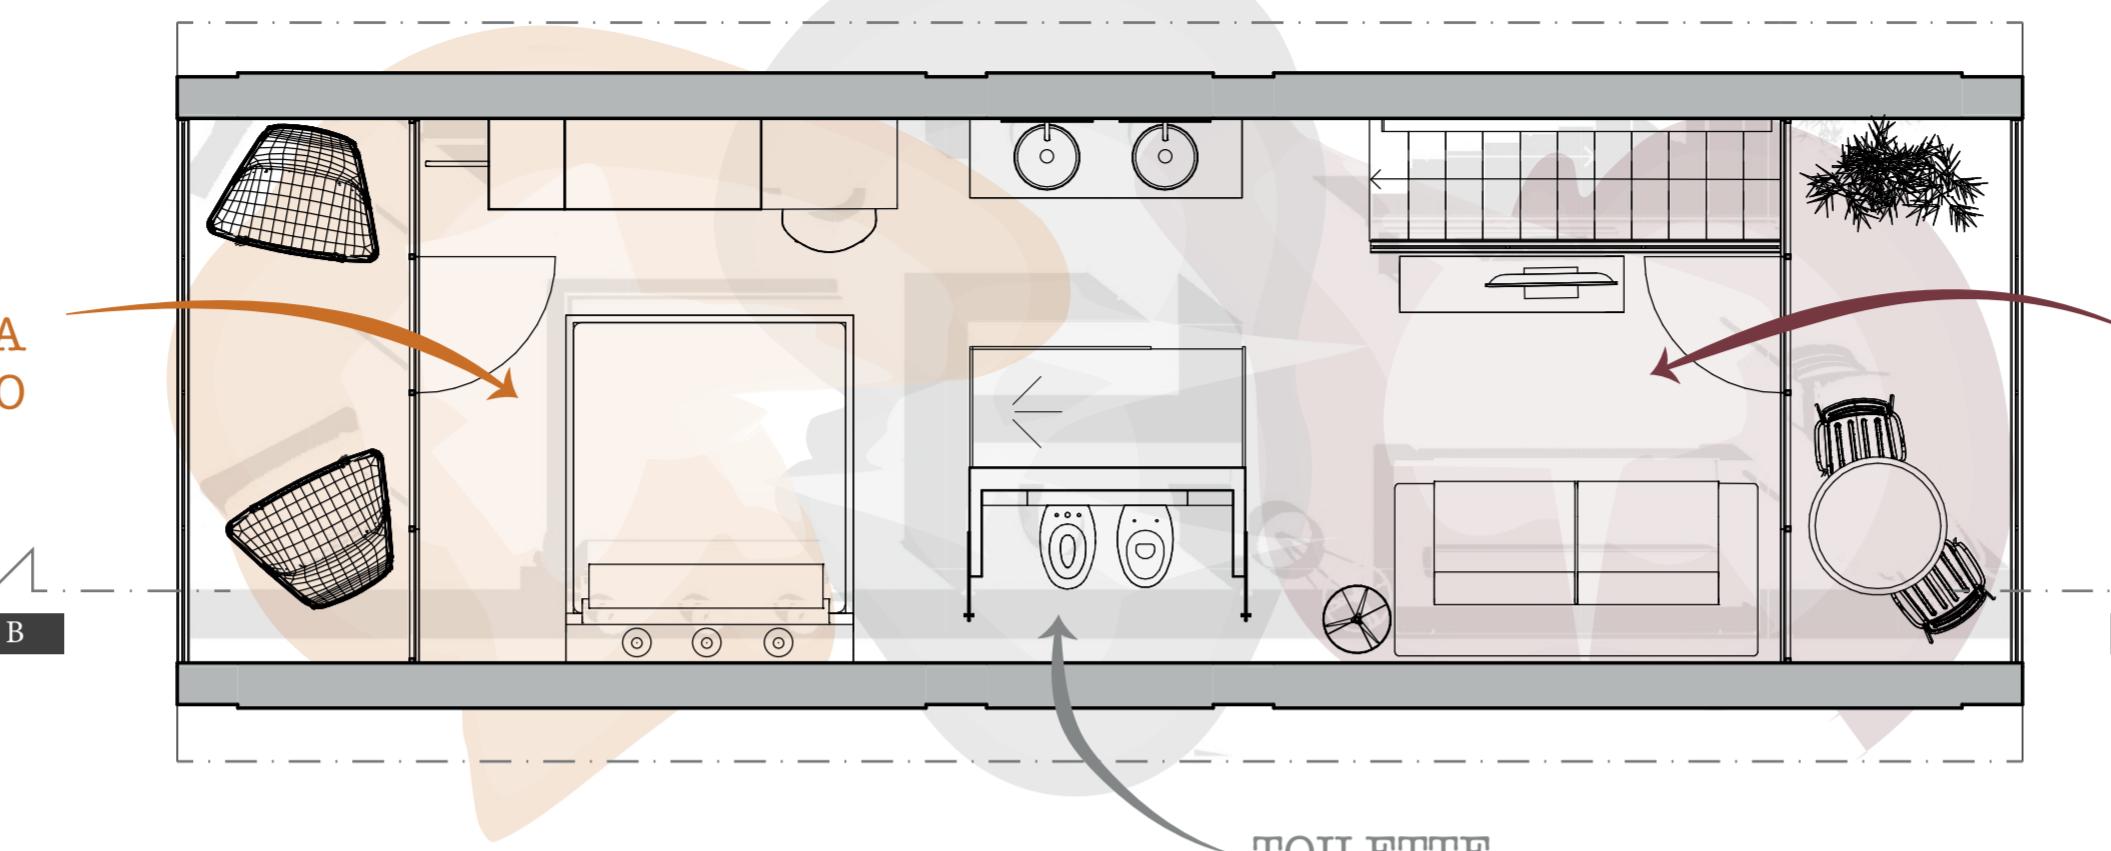


LIVING / CAMERA
DI SERVIZIO


pianta II piano




prospetto ovest

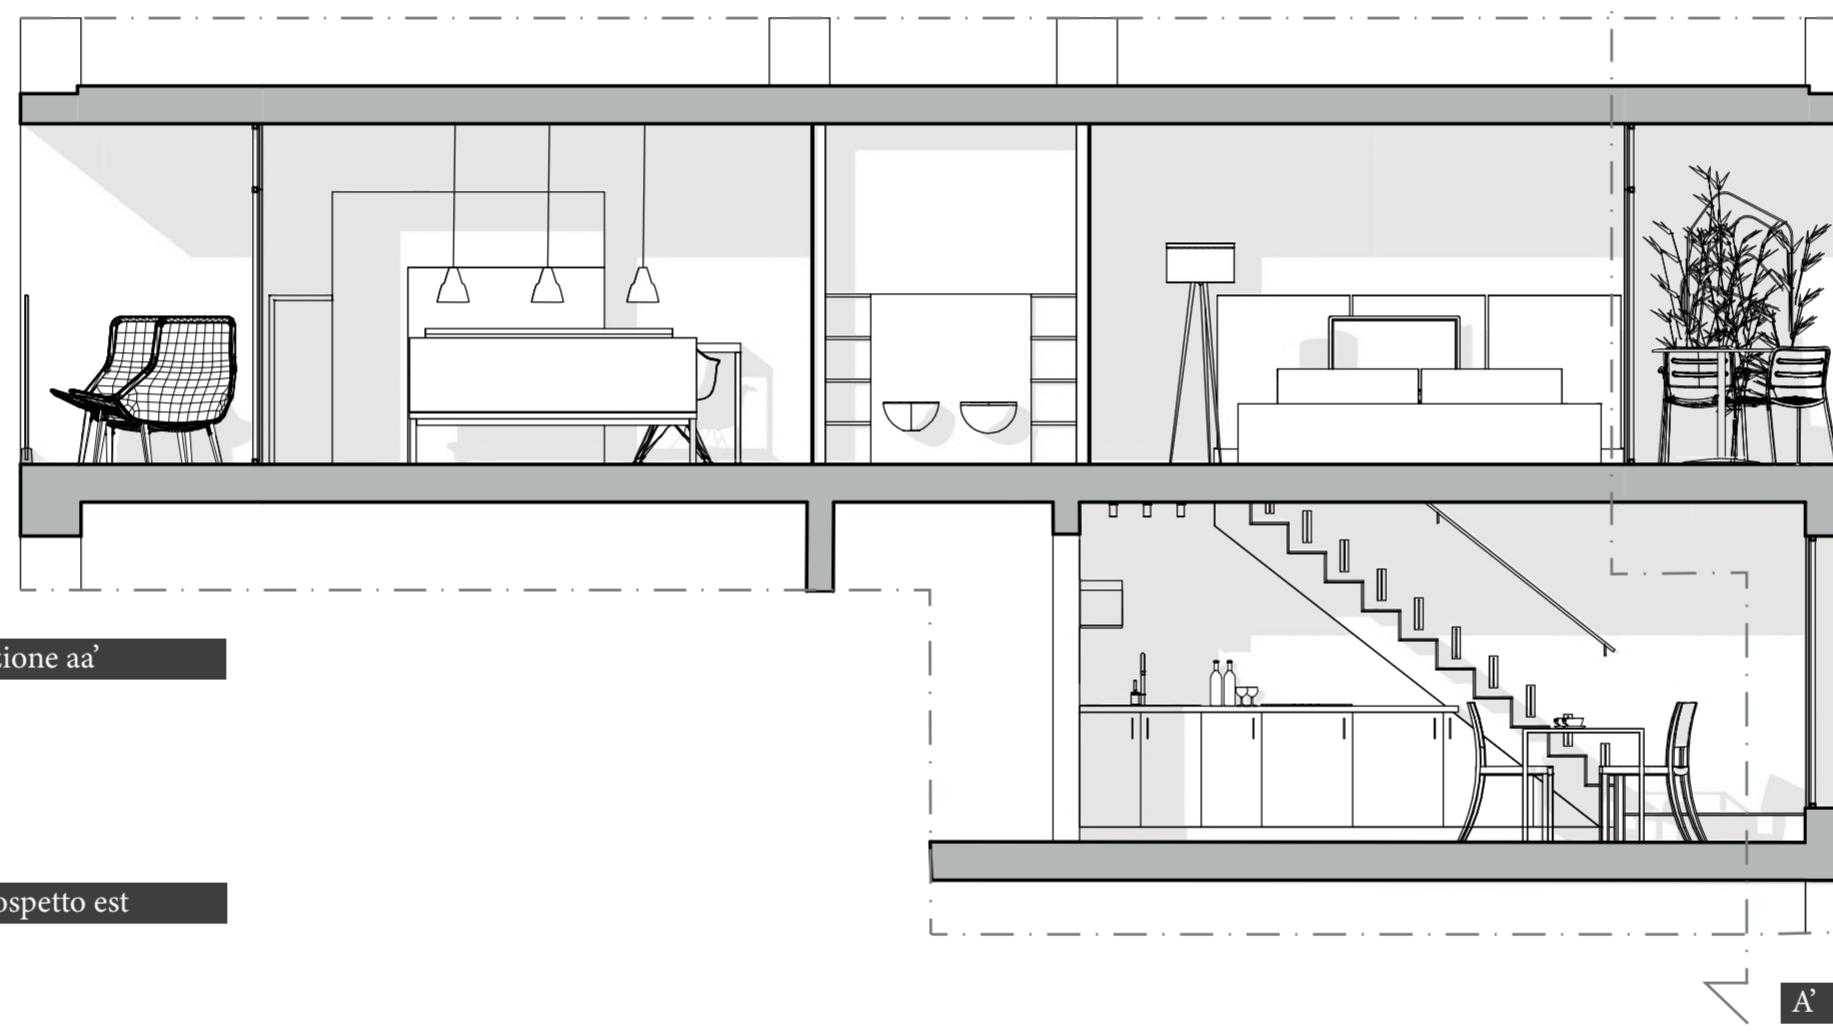

sezione aa'

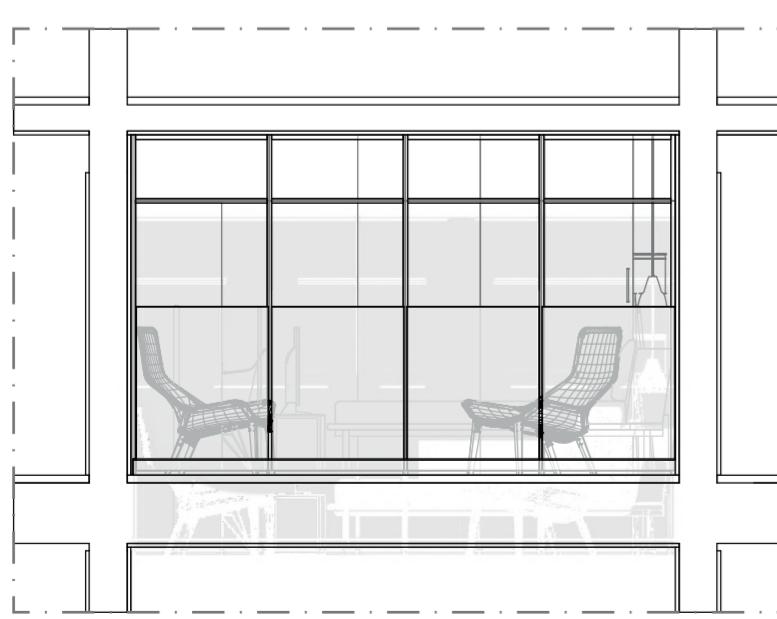


prospetto est

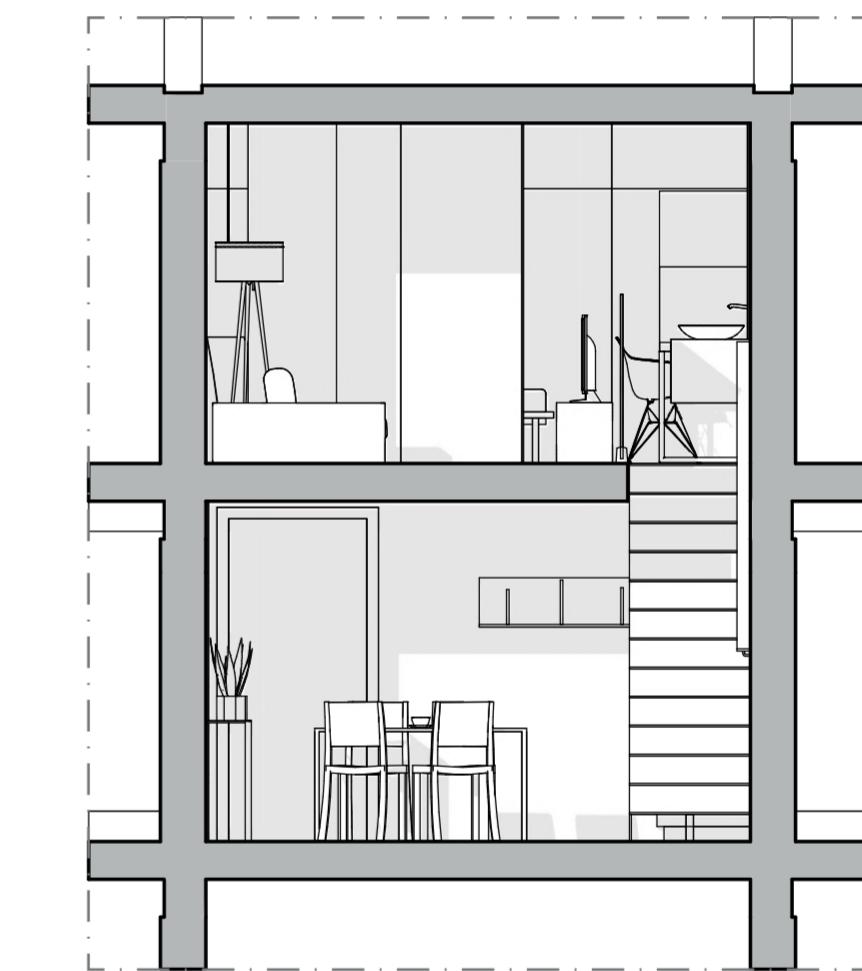

sezione bb'

CUCINA

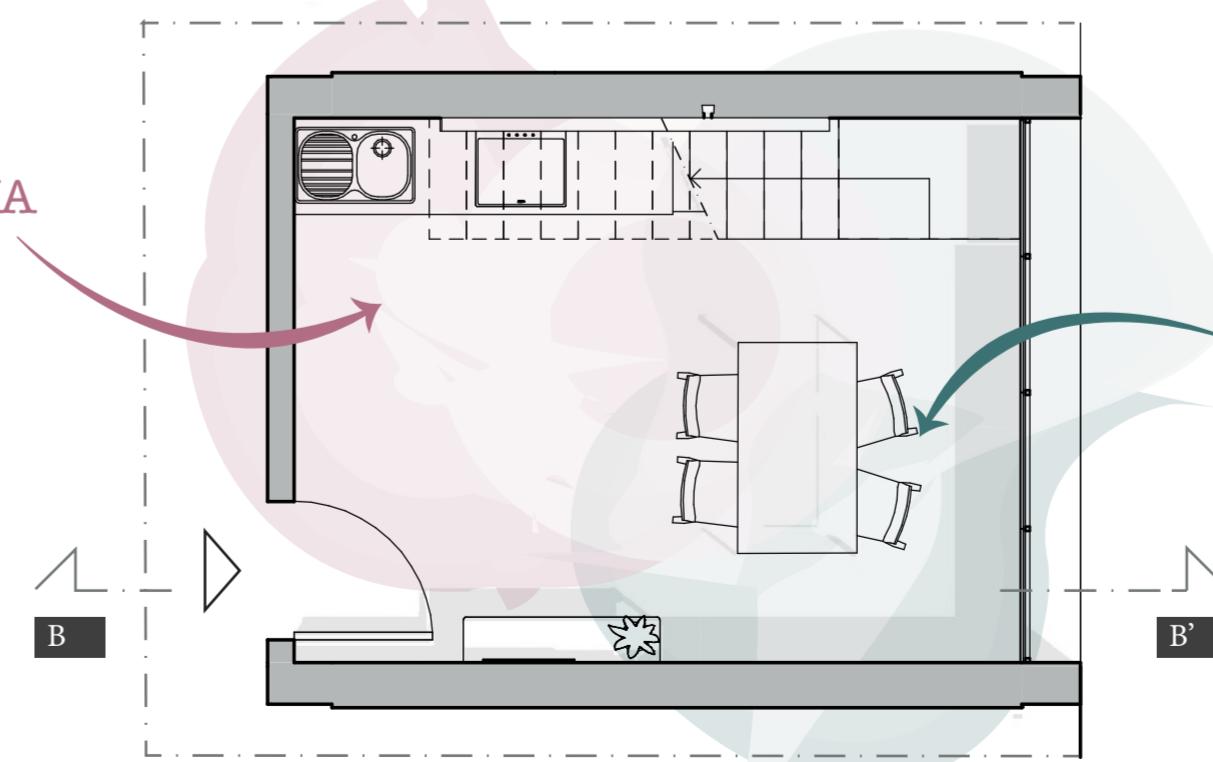

SALA DA
PRANZO

pianta I piano




breezy suite

L-Mode

L-Mode è un armadio costituito da moduli scomponibili, che consentono vasta mobilità nell'arredamento di una stanza. In questa variante fa da armadio, ripostiglio, attaccapanni e scrivania, consentendo di condensare diverse funzioni in uno spazio ridotto.

Struttura e ante sono costituite da un multistrato di betulla, ma per il modulo quadrato centrale è possibile sostituire le ante con vetro trasparente o specchiante e inserire all'interno un led che porti la luce necessaria.

Il tubo appendiabiti e il sostegno della scrivania sono profilati verniciabili con numerose lacche ecosostenibili.

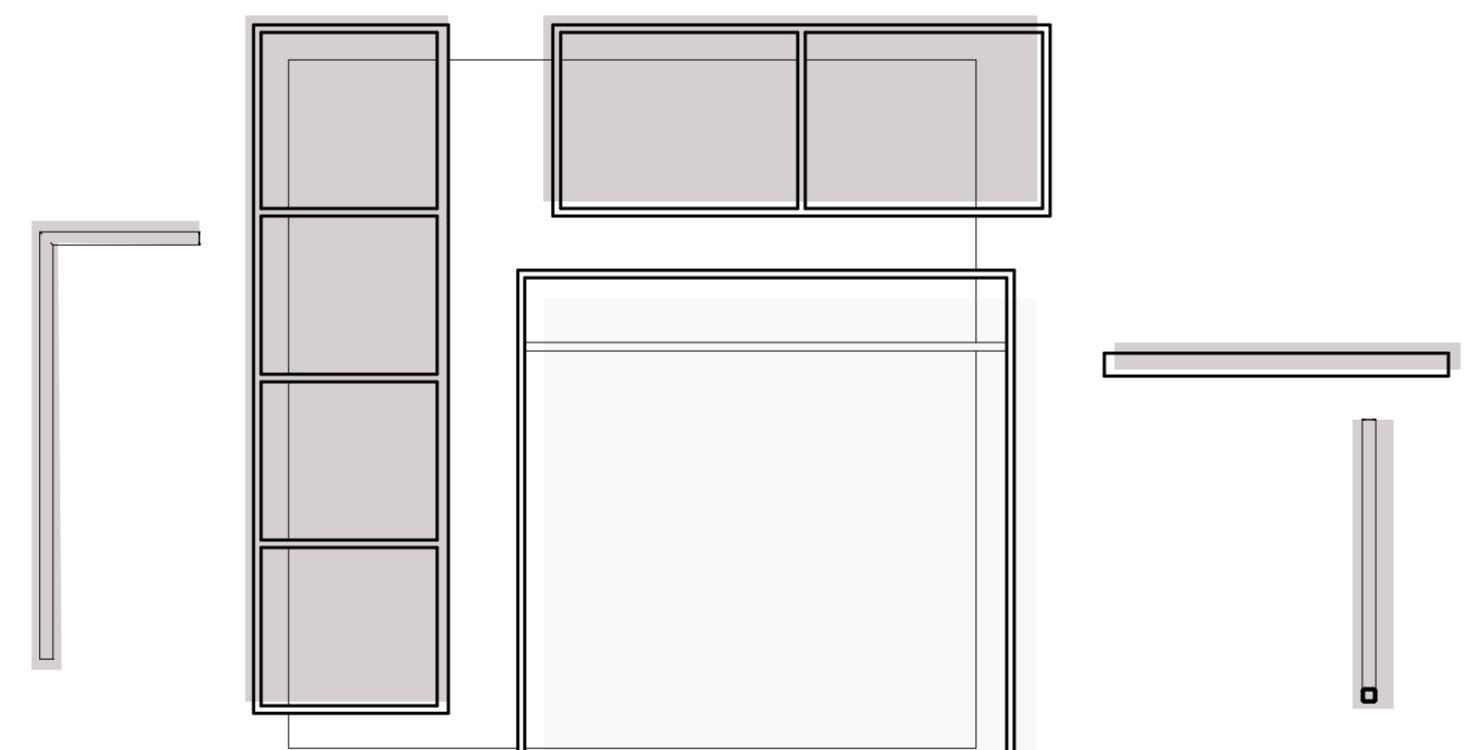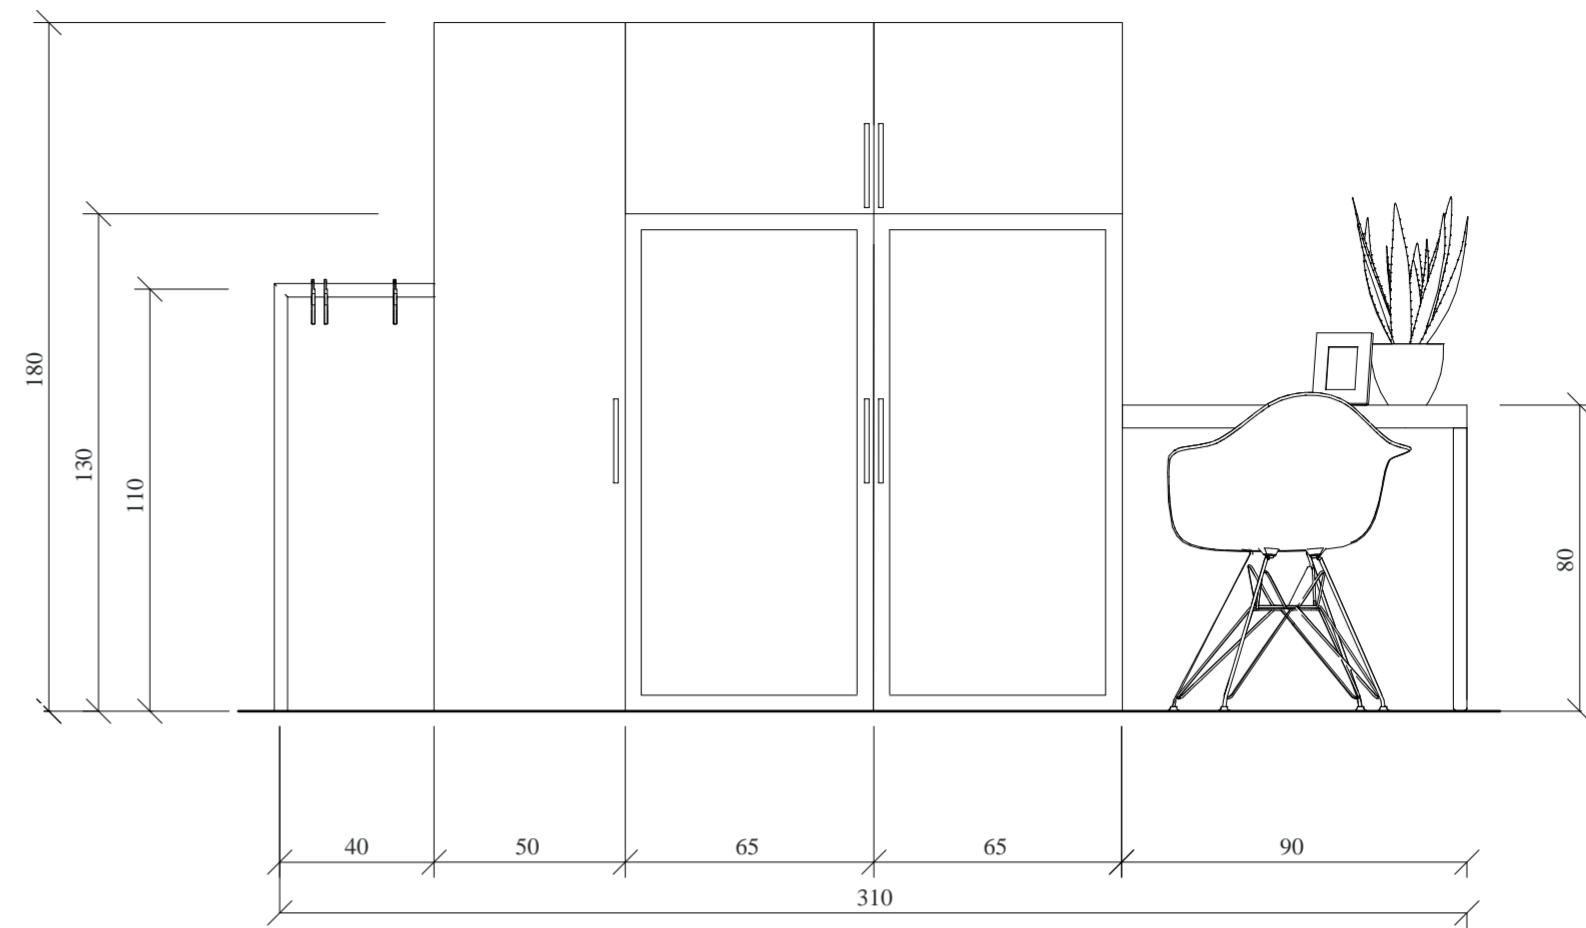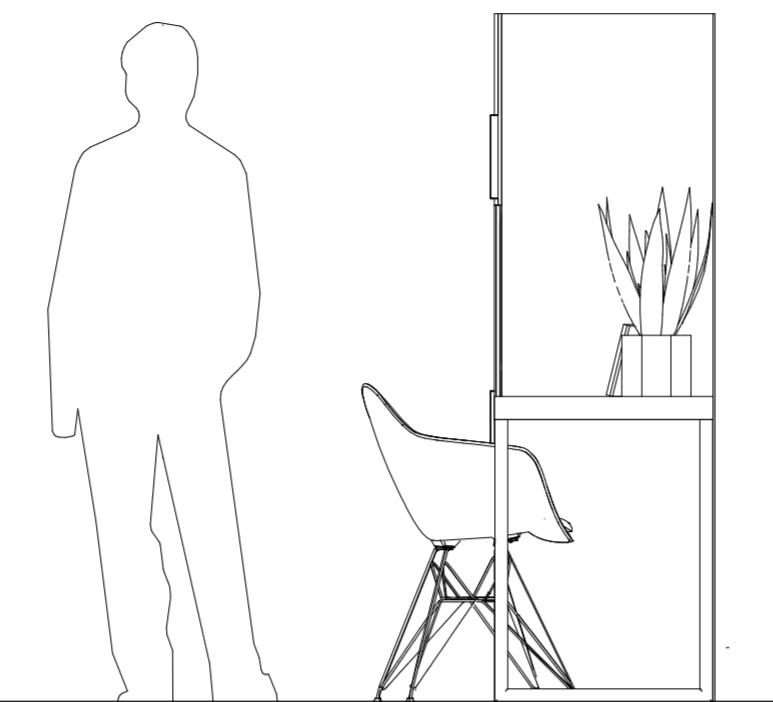

I moduli scomponibili e i pezzi complementari.

